


F-1

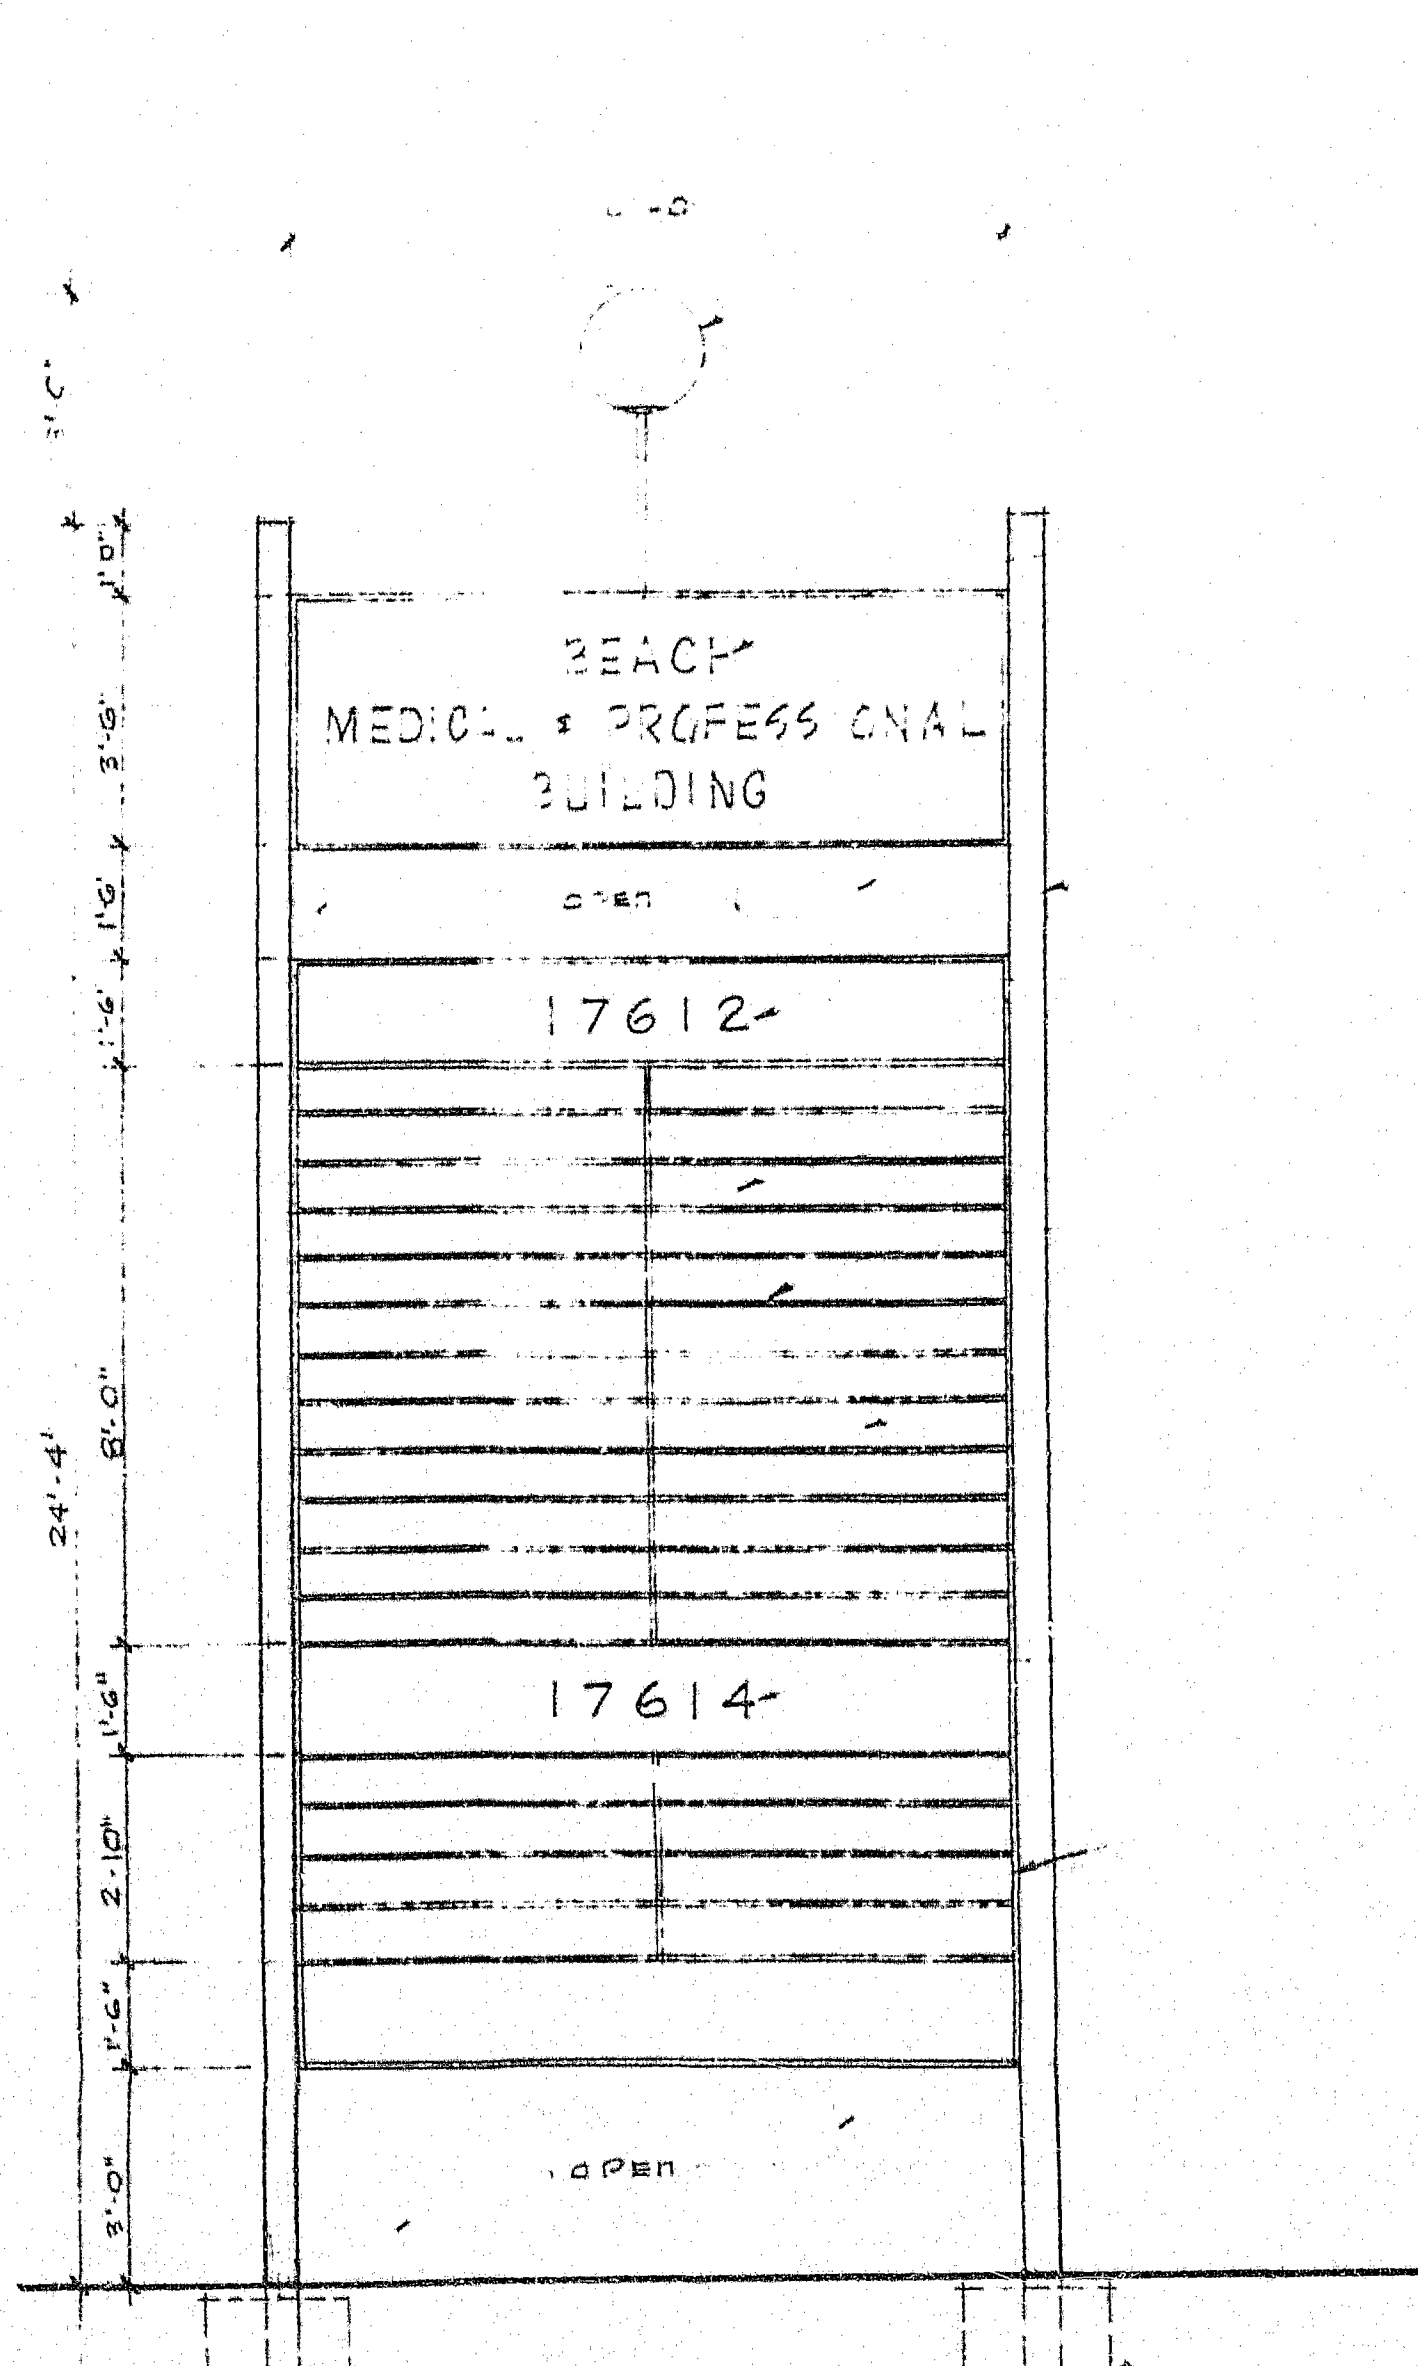

NOTE
ALL WORK TO BE W/ APPROVED
CONTRACTOR TO TAKE
NECESSARY MEASURES TO EXIST
COND.

6" Ø GLASS SPHERE LIGHTED
W/ 180 W/ 75 WATT

6" H PLEXIGLAS LETTERS

SIGN TO BE LIGHTED W/ 400 V.A.
INSTANT START FLUO. TUBES &
W/ 180 W/ 75 WATT

10 W/ 24" COLUMNS

6" H PLEXIGLAS LETTERS

SIGN FACE TO BE 1/8" FLAT
WHITE PLASTIC, 1/8" SECTIONAL
SECTIONAL AS REQ. TO SERVICE
UNIT

DIVIDER STRIPS TO BE 1/8" THICK
BY 1/2" WIDE BLACK PLEXIGLAS
GLUED TO FACE

LETTERS FOR SUITE NAMES
TO BE PAINTED W/ WEATHERPROOF
YET REMOVABLE TYPE PAINT
(FOR BIDDING PURPOSES, AS TRACTING
TO ASSUME 1/2 OF SUITES TO BE PAINTED)

6" H PLEXIGLAS LETTERS

ALL METAL WORK & CABINET TO
BE 24 GA. G.I. METAL W/ ANGLE
IRON FRAMES AS REQ. FOR
FIRM SUPPORT

31" Ø Ø
CONC. FOOTING

SIGN FOR A MEDICAL BUILDING
FOR DR. L.G. NELSON
17612 BEACH BLVD.
HUNTINGTON BEACH, CALIF.

BEACH
MEDICAL & PROFESSIONAL
BUILDING

SIGN TO BE LIGHTED W/ 420 M.A.
INSTANT START FLOWZ. TUBES @
10" O.C. MIN.

10 WF 29 COLUMNS

6" HI PLEXIGLAS LETTERS

SIGN FACE TO BE 3/16" FLAT
WHITE PLASTIC IN REMOVABLE
SECTIONS AS REQ. TO SERVICE
UNIT.

DIVIDER STRIPS TO BE 1/8" THICK
BY 1/2" WIDE BLACK PLEXIGLAS
GLUED TO FACE

LETTERS FOR SUITE NAMES
TO BE PAINTED W/ WEATHERPROOF
YET REMOVABLE TYPE PAINT
(FOR BIDDING PURPOSES, CONTRACTOR
TO ASSUME 1/2 OF SUITES TO BE PAINTED)

6" HI PLEXIGLAS LETTERS


ALL METAL WORK & CABINET TO
BE 24 GA. G.I. METAL W/ ANGLE
IRON FRAMES AS REQ. FOR
FIRM SUPPORT.

3'-0" ϕ
CONC. FOOTINGS

SIGN FOR A MEDICAL BUILDING
for DR. L.G. NELSON
17612 BEACH BLVD.
HUNTINGTON BEACH, CALIF
DATE: 4-11-63

ELEVATION 3/8" = 1'-0"
(OPPOSITE SIDE STAIRS)

F-2

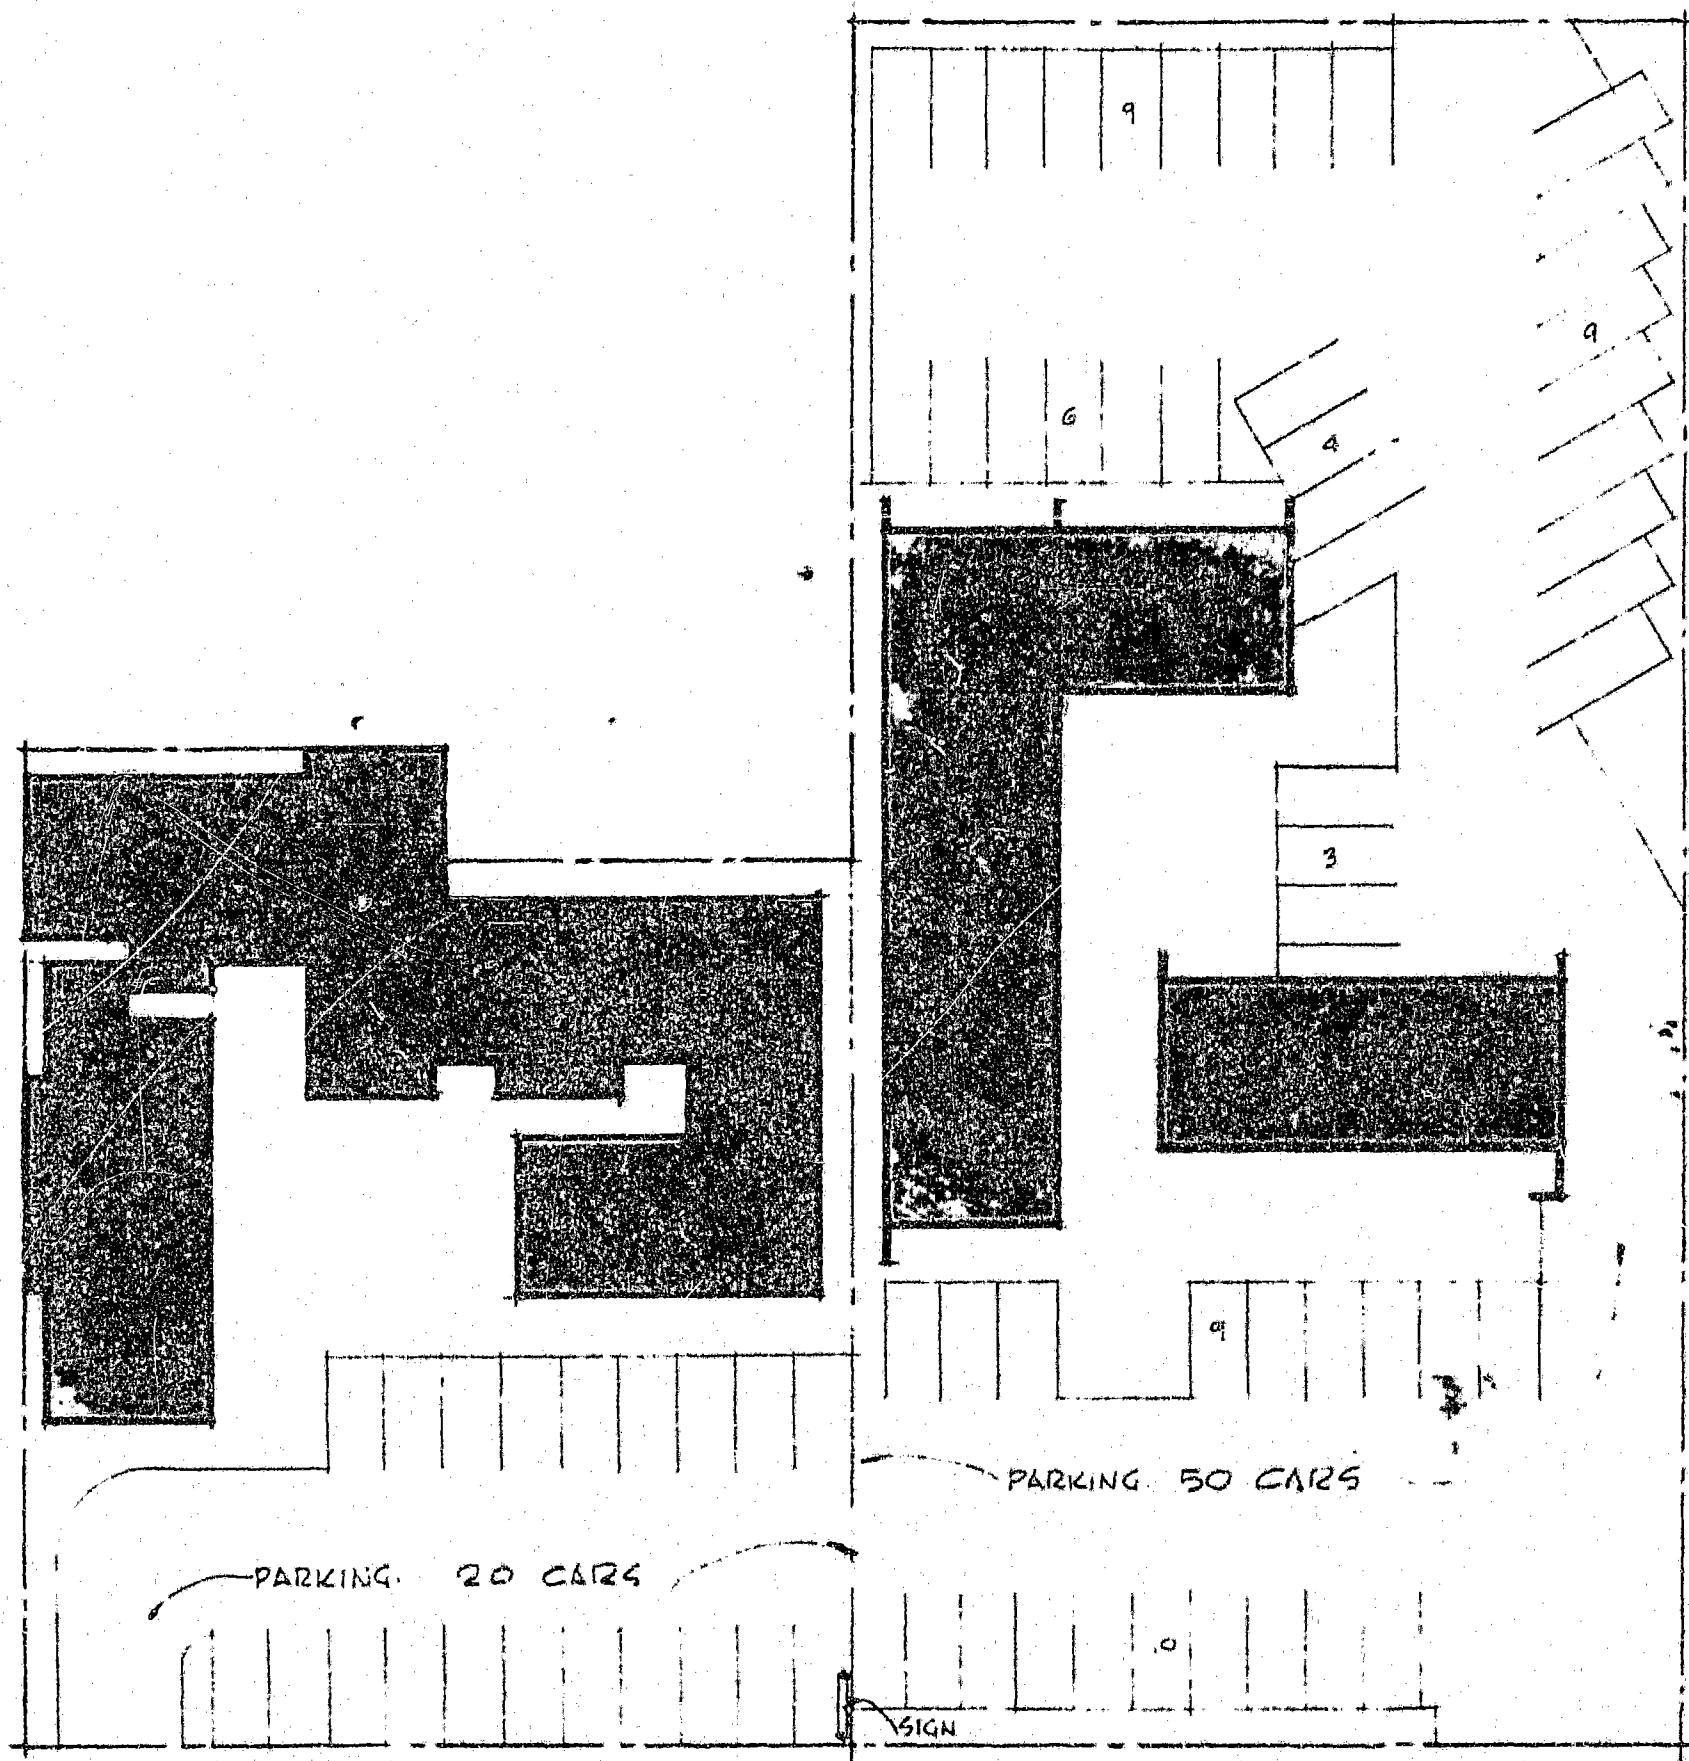

← ——— BEACH BLVD. ——— →
 PLOT PLAN 1" = 30'-0"

A MEDICAL BUILDING FOR
 DR. LEON G NELSON
 17614 BEACH BLVD. HUNTINGTON BEACH CALIF.

WM. P. FICKER, A. I. A.

446 NORTH NEWPORT BLVD.
 NEWPORT BEACH, CALIFORNIA