


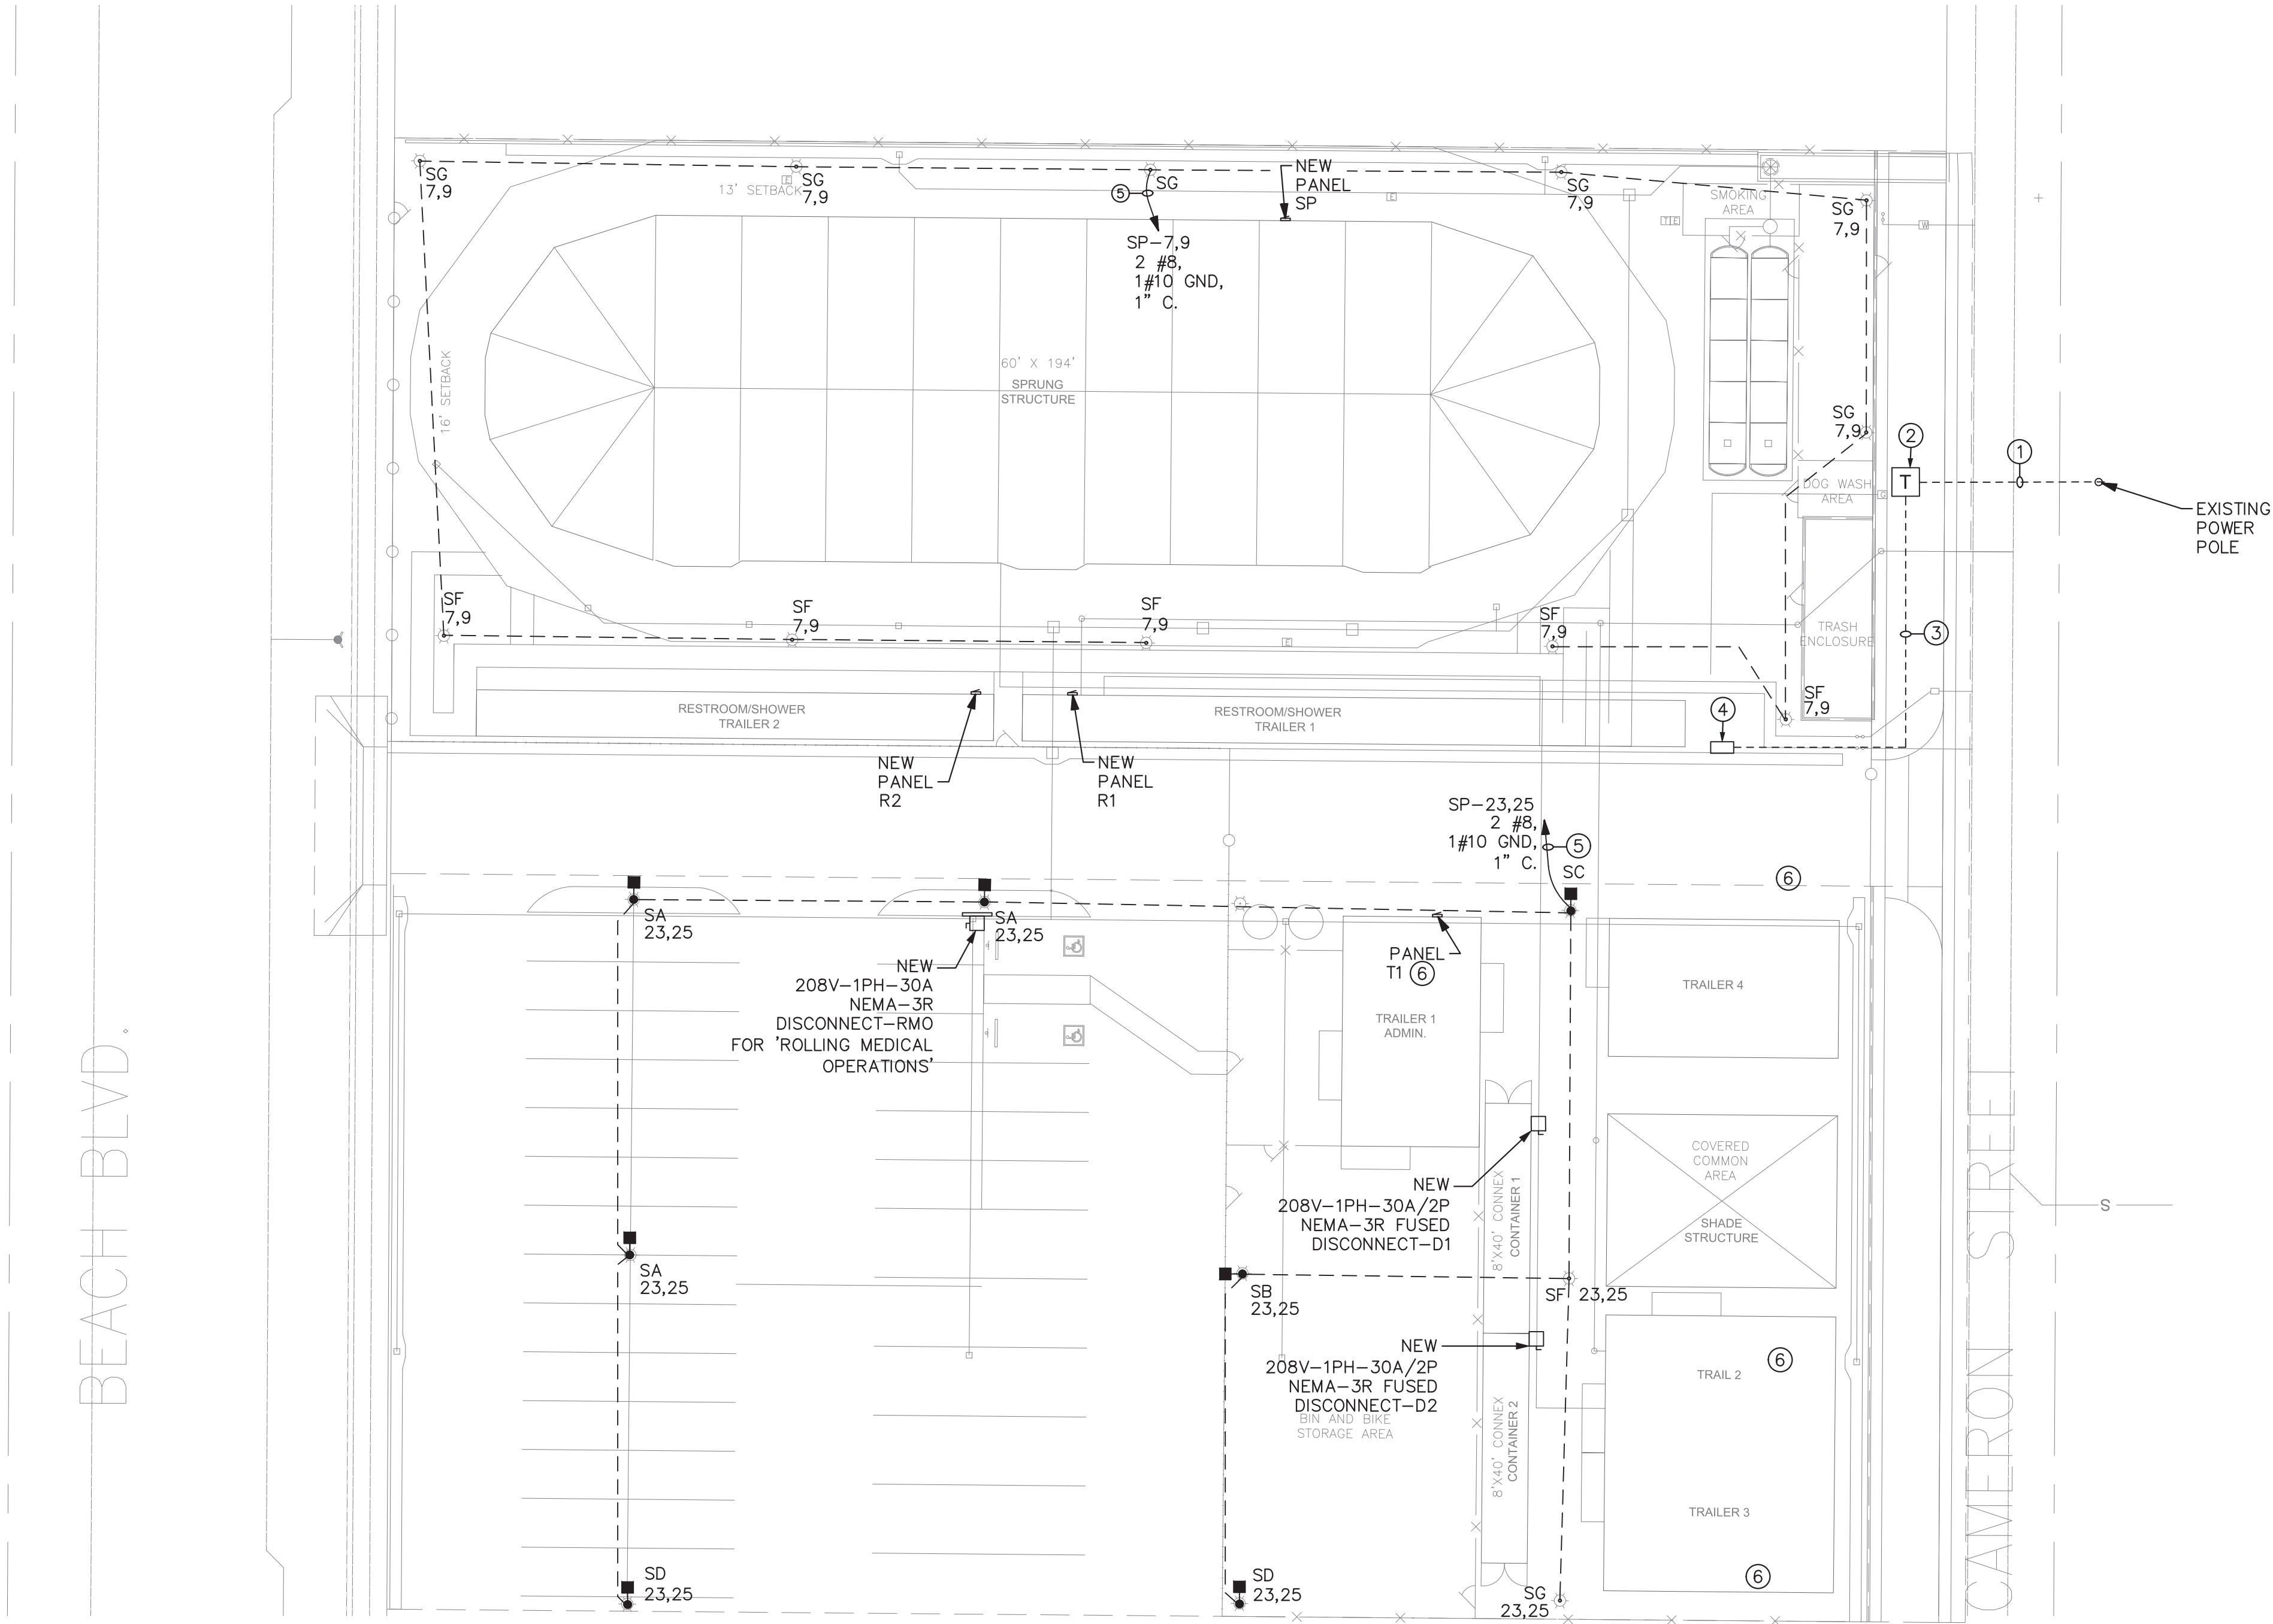

1 ELECTRICAL SITE PLAN
SCALE: 1"= 20'

GENERAL NOTES

- A. ALL EXTERIOR LIGHT FIXTURES TO COMPLY WITH LOCAL NIGHT SKY ORDINANCE.
- B. ALL EXTERIOR LIGHTING AND SIGNAGE TO BE FED WITH #10 CU. U.N.O.
- C. ALL EXTERIOR ELECTRICAL EQUIPMENT TO BE NEMA-3R RATED.
- D. CONTRACTOR TO COORDINATE EXACT SITE LIGHTING FIXTURE LOCATIONS WITH LANDSCAPE DRAWINGS.
- E. ALL FIXTURES INSTALLED OUTDOORS SHALL BE RATED FOR DAMP/WET LOCATIONS AS REQUIRED. THE CONTRACTOR SHALL COORDINATE DAMP/WET LOCATION RATING PER NEC ARTICLE 410-4. ALL INSTALLATIONS SHALL CONFORM TO NEC ARTICLE 410, ALL SUB ARTICLES.
- F. FIRE ALARM EQUIPMENT SHALL BE COORDINATED FOR EXACT LOCATION AND REQUIREMENTS WITH FIRE MARSHALL.
- G. ALL PVC CONDUIT MUST HAVE A MINIMUM OF #12 CU. GROUND CONDUCTOR.
- H. CONTRACTOR SHALL BE RESPONSIBLE FOR COORDINATION AND SCHEDULING WITH POWER AND TELEPHONE UTILITY COMPANIES INCLUDING PROVIDING (2) COMPLETE SETS OF DRAWINGS TO EACH COMPANY. ALL WORK SHALL BE INSTALLED PER EACH UTILITY COMPANIES FINAL DESIGN DRAWINGS.
- I. ELECTRICAL CONTRACTOR SHALL COORDINATE EXACT LOCATIONS AND MOUNTING HEIGHTS OF ALL EXTERIOR LIGHT FIXTURES WITH ARCHITECTURAL DRAWINGS.

KEYED NOTES

- 1. PRIMARY FEEDERS PER POWER COMPANY REQUIREMENTS. REFER TO ONE-LINE DIAGRAM.
- 2. PROPOSED NEW PAD MOUNTED POWER COMPANY TRANSFORMER. PROVIDE PAD PER POWER COMPANY REQUIREMENTS. MAINTAIN 10'-0" FRONT CLEARANCE, 3'-0" SIDES AND REAR CLEARANCE.
- 3. NEW SECONDARY FEEDERS PER POWER COMPANY REQUIREMENTS. REFER TO ONE-LINE DIAGRAM.
- 4. NEW FLOOR MOUNTED FREE STANDING SERVICE ENTRANCE SECTION IN NEMA-3R ENCLOSURE. REFER TO ONE-LINE DIAGRAM AND LOAD CALCULATIONS.
- 5. CIRCUIT THROUGH PHOTOCELL ON/PHOTOCELL OFF. PROVIDE 7 DAY, 2 CHANNEL TIMECLOCK WITH OVERRIDE SWITCH FOR OPTIONAL CONTROL AT PANEL. PROVIDE 12' OF WIRE RUN FROM PANEL TO TIMECLOCK TO LIMIT FAULT CURRENT TO BE LESS THAN 5000 AMPS
- 6. TRAILER PANELS T1, T2, T3 AND T4 PROVIDED WITH TRAILER. ELECTRICAL CONTRACTOR SHALL MAKE FINAL CONNECTION TO TRAILER PANEL.

NOTE

ALL OF THE PANELS & DISCONNECTS WILL BE FED FROM NEW S.E.S



innovation | versatility | reliability

TOLL FREE: 1-800-528-9899
or (403) 601-2292 www.sprung.com



DESIGN LOADS

STRUCTURE LOCATION: HUNTINGTON BEACH, CA
BUILDING CODE: IBC 2018/CBC 2019
WIND SPEED: 106 mph 3 SEC GUST
RISK CATEGORY: II EXPOSURE C
GROUND SNOW LOAD: NA
(SEE SNOW SHED REPORT)



940 E Elm Avenue
Salt Lake City, Utah 84106
Phone: (801) 486-6848




SIGNATURE SERIES

REV MM/DD/YY BY DESCRIPTION
This drawing is protected by copyright in the United States of America, Canada and all other countries of the world. It, and all of the designs, technical data and engineering services represented by it and originated or rendered by SPRUNG INSTANT STRUCTURES INC. are the exclusive property of SPRUNG INSTANT STRUCTURES INC. and must neither be used in manufacturing nor disclosed nor reproduced in whole or in part except with the prior written consent of SPRUNG INSTANT STRUCTURES INC. Any copying of this drawing in whole or in part and any use of it to construct the subject matter illustrated in it without prior written permission of SPRUNG INSTANT STRUCTURES INC. is prohibited.

17631 CAMERON LANE
HUNTINGTON BEACH, CA 92647

ELECTRICAL
SITE PLAN

DRAWN BY:	DATE:
SCALE:	DRAWING #
SPRUNG WO:	E0.1

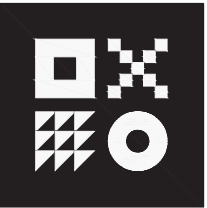

ARDEBILI
Engineering

Project Number: 20393 | Project Manager: FH
8190 E Indian School Rd. Suite 205, Scottsdale, AZ 85251
P: 480.626.7072 | ardebilieng.com



Specifications

Diameter: 8" Round
(203 mm)
Height: 42"
(1067 mm)
Weight (max): 27 lbs
(12.25 kg)



EXAMPLE: DSXB LED 16C 700 40K SYM MVOLT DDBXD									
Series	LEDs	Drive current	Color temperature	Distribution	Voltages	Control options	Other options	Finish	Notes
DSXB LED	Asymmetric 12C 12 LED Symmetric 16C 16 LED ¹	350 350 mA 450 450 mA ¹⁴ 530 530 mA 700 700 mA	30K 3000 K 40K 4000 K 50K 5000 K AMBP Amber phosphor converted AMBLW Amber limited wavelength ¹⁴	ASY Asymmetric ¹ SYM Symmetric ²	MVOLT ¹ 120 ¹ 208 ¹ 240 ¹ 277 ¹ 347 ¹	Shipped installed PE Photometric cell, bottom type DMG 00-10V dimming wires pulled outside fixture (for use with an external control, ordered separately) ELCW Emergency battery backup ¹	Shipped installed SF Single face (120, 277, 347V) ¹ DF Double face (208, 240V) ¹ H24 24" overall height H30 30" overall height H36 36" overall height FG Ground-fault protection outlet LAB Wireless anchor bolts L/AB4 4-bolt retrofit base without anchor bolts ¹	DWBKD White DNAXD Natural aluminum DBBKD Dark bronze DBLKD Black DBRDK Textured dark bronze DBLTKD Textured black DNATKD Textured natural aluminum DWHGKD Textured white	

Accessories

MMAB U Anchor bolts for 6000¹

NOTES

- Only available in the 12C, ASY version.
- Only available in the 16C, SYM version.
- Only available with 400 AMBW version.
- Not available with ELCW.
- MOCK driver operates on any line voltage from 120-277V (50/60 Hz). Specify 120, 208, 240 or 277 options only when ordering with fusing (SF, DF) options, or photocell (PE) options.
- Not available with 347V. Not available with fusing. Not available with 400 AMBLW.
- Single face (SF) requires 120, 277, or 347 voltage option. Double face (DF) requires 208 or 240 voltage option.
- MMAB U not available with LAB4 option.




One Lithonia Way • Cary, Georgia 30012 • Phone: 800.279.8241 • www.lithonia.com
© 2012-2018 Acuity Brands Lighting, Inc. All rights reserved.

D-Series Size 0 LED Area Luminaire




Specifications

EPA: 0.95 ft²
(0.09 m²)
Length: 26"
(661 mm)
Width: 13"
(330 mm)
Height: 3"
(76 mm)
Height: 7"
(178 mm)
Weight (max): 1.6 lbs
(0.72 kg)

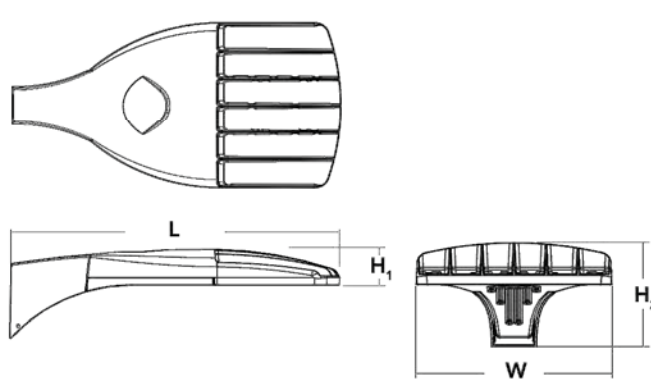


EXAMPLE: DSX0 LED P6 40K T3M MVOLT SPA NLTAIR2 PIRHN DDBXD									
Series	LEDs	Color temperature	Distribution	Voltage	Mounting				
DSX0 LED	Forward optics P1 P4 ¹ P7 ¹ P2 P5 P3 P6 Retained optics P10 ¹ P12 ¹ P11 ¹ P13 ¹²	30K 3000 K 40K 4000 K 50K 5000 K	T1S Type I short (Automotive) T2S Type II short T2M Type II medium T3M Type III medium T4M Type IV medium TFM Forward throw medium TSVS Type V very short ¹	T5S Type V short ¹ T5M Type V medium ¹ T5W Type V wide ¹ 240 ¹ 277 ¹ 347 ¹ 480 ¹	MVOLT ¹⁴ 120 ¹ 208 ¹ 240 ¹ 277 ¹ 347 ¹ 480 ¹	Shipped included SPA Square pole mounting RPA Round pole mounting ¹ HBA Wall bracket ¹ SPUMA Square pole universal mounting adapter ¹ RPUABA Round pole universal mounting adapter ¹	Shipped separately KMA6 DDBXD U Mast arm mounting bracket adaptor (specify finish) ¹	DBBKD Dark bronze DBLKD Black DNAXD Natural aluminum DWBKD White DBRDK Textured dark bronze DBLTKD Textured black DNATKD Textured natural aluminum DWHGKD Textured white	
Control options						Other options			
Shipped installed NLTAIR2 HSLight AIR generation 2 enabled ^{11,12} PIRHN Network, high-low motion/ambient sensor, 15-30' mounting height, ambient sensor enabled at 30' ¹³ PER HEMA twist-lock receptacle only (control ordered separately) ¹³ PER5 Five-pin receptacle only (control ordered separately) ^{13,14} PER7 Seven-pin receptacle only (leads exit fixture) (control ordered separately) ^{13,14} DMG 0-10V dimming extend out back of housing for external control (control ordered separately) ¹						Other options PIR High/low, motion/ambient sensor, 0-15' mounting height, ambient sensor enabled at 30' ¹³ PIRHN High/low, motion/ambient sensor, 15-30' mounting height, ambient sensor enabled at 30' ¹³ PIRHN5V High/low, motion/ambient sensor, 0-15' mounting height, ambient sensor enabled at 30' ¹³ PIRHN7CV High/low, motion/ambient sensor, 15-30' mounting height, ambient sensor enabled at 30' ¹³ FAO Field adjustable output ¹			
Shipped separately BS Bed spikes ¹⁵ ECS External glare shield						Finish options			
						Finish colors			

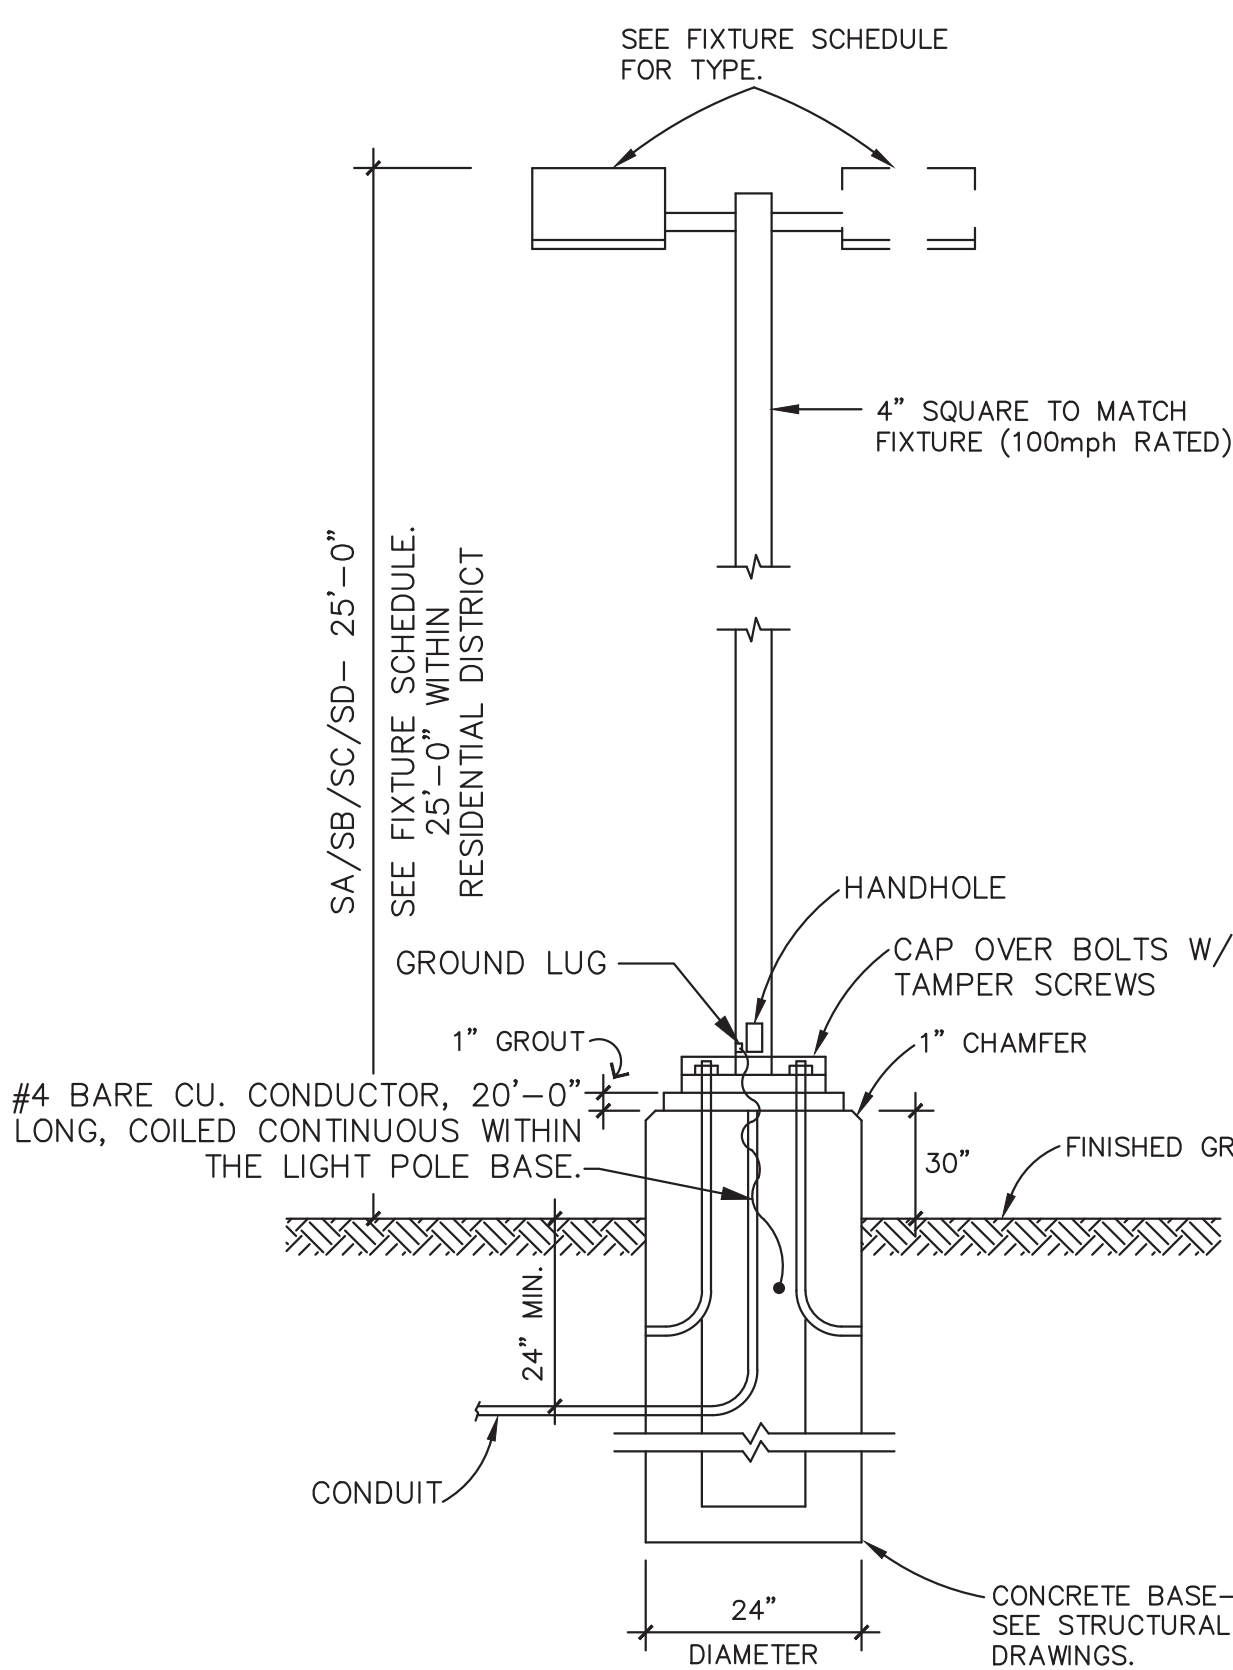

LIGHT POLE AND FIXTURE 'SA/SB/SC/SD'

NOTE:

CONTRACTOR SHALL PROVIDE NEW POLE BASES WHERE INDICATED ON PLANS. LIGHTING FIXTURE POLE DETAILS AND DESCRIPTIONS ARE FOR ELECTRICAL REFERENCES ONLY. PLEASE REFER TO STRUCTURAL DRAWINGS FOR POLE BASE DETAILS.

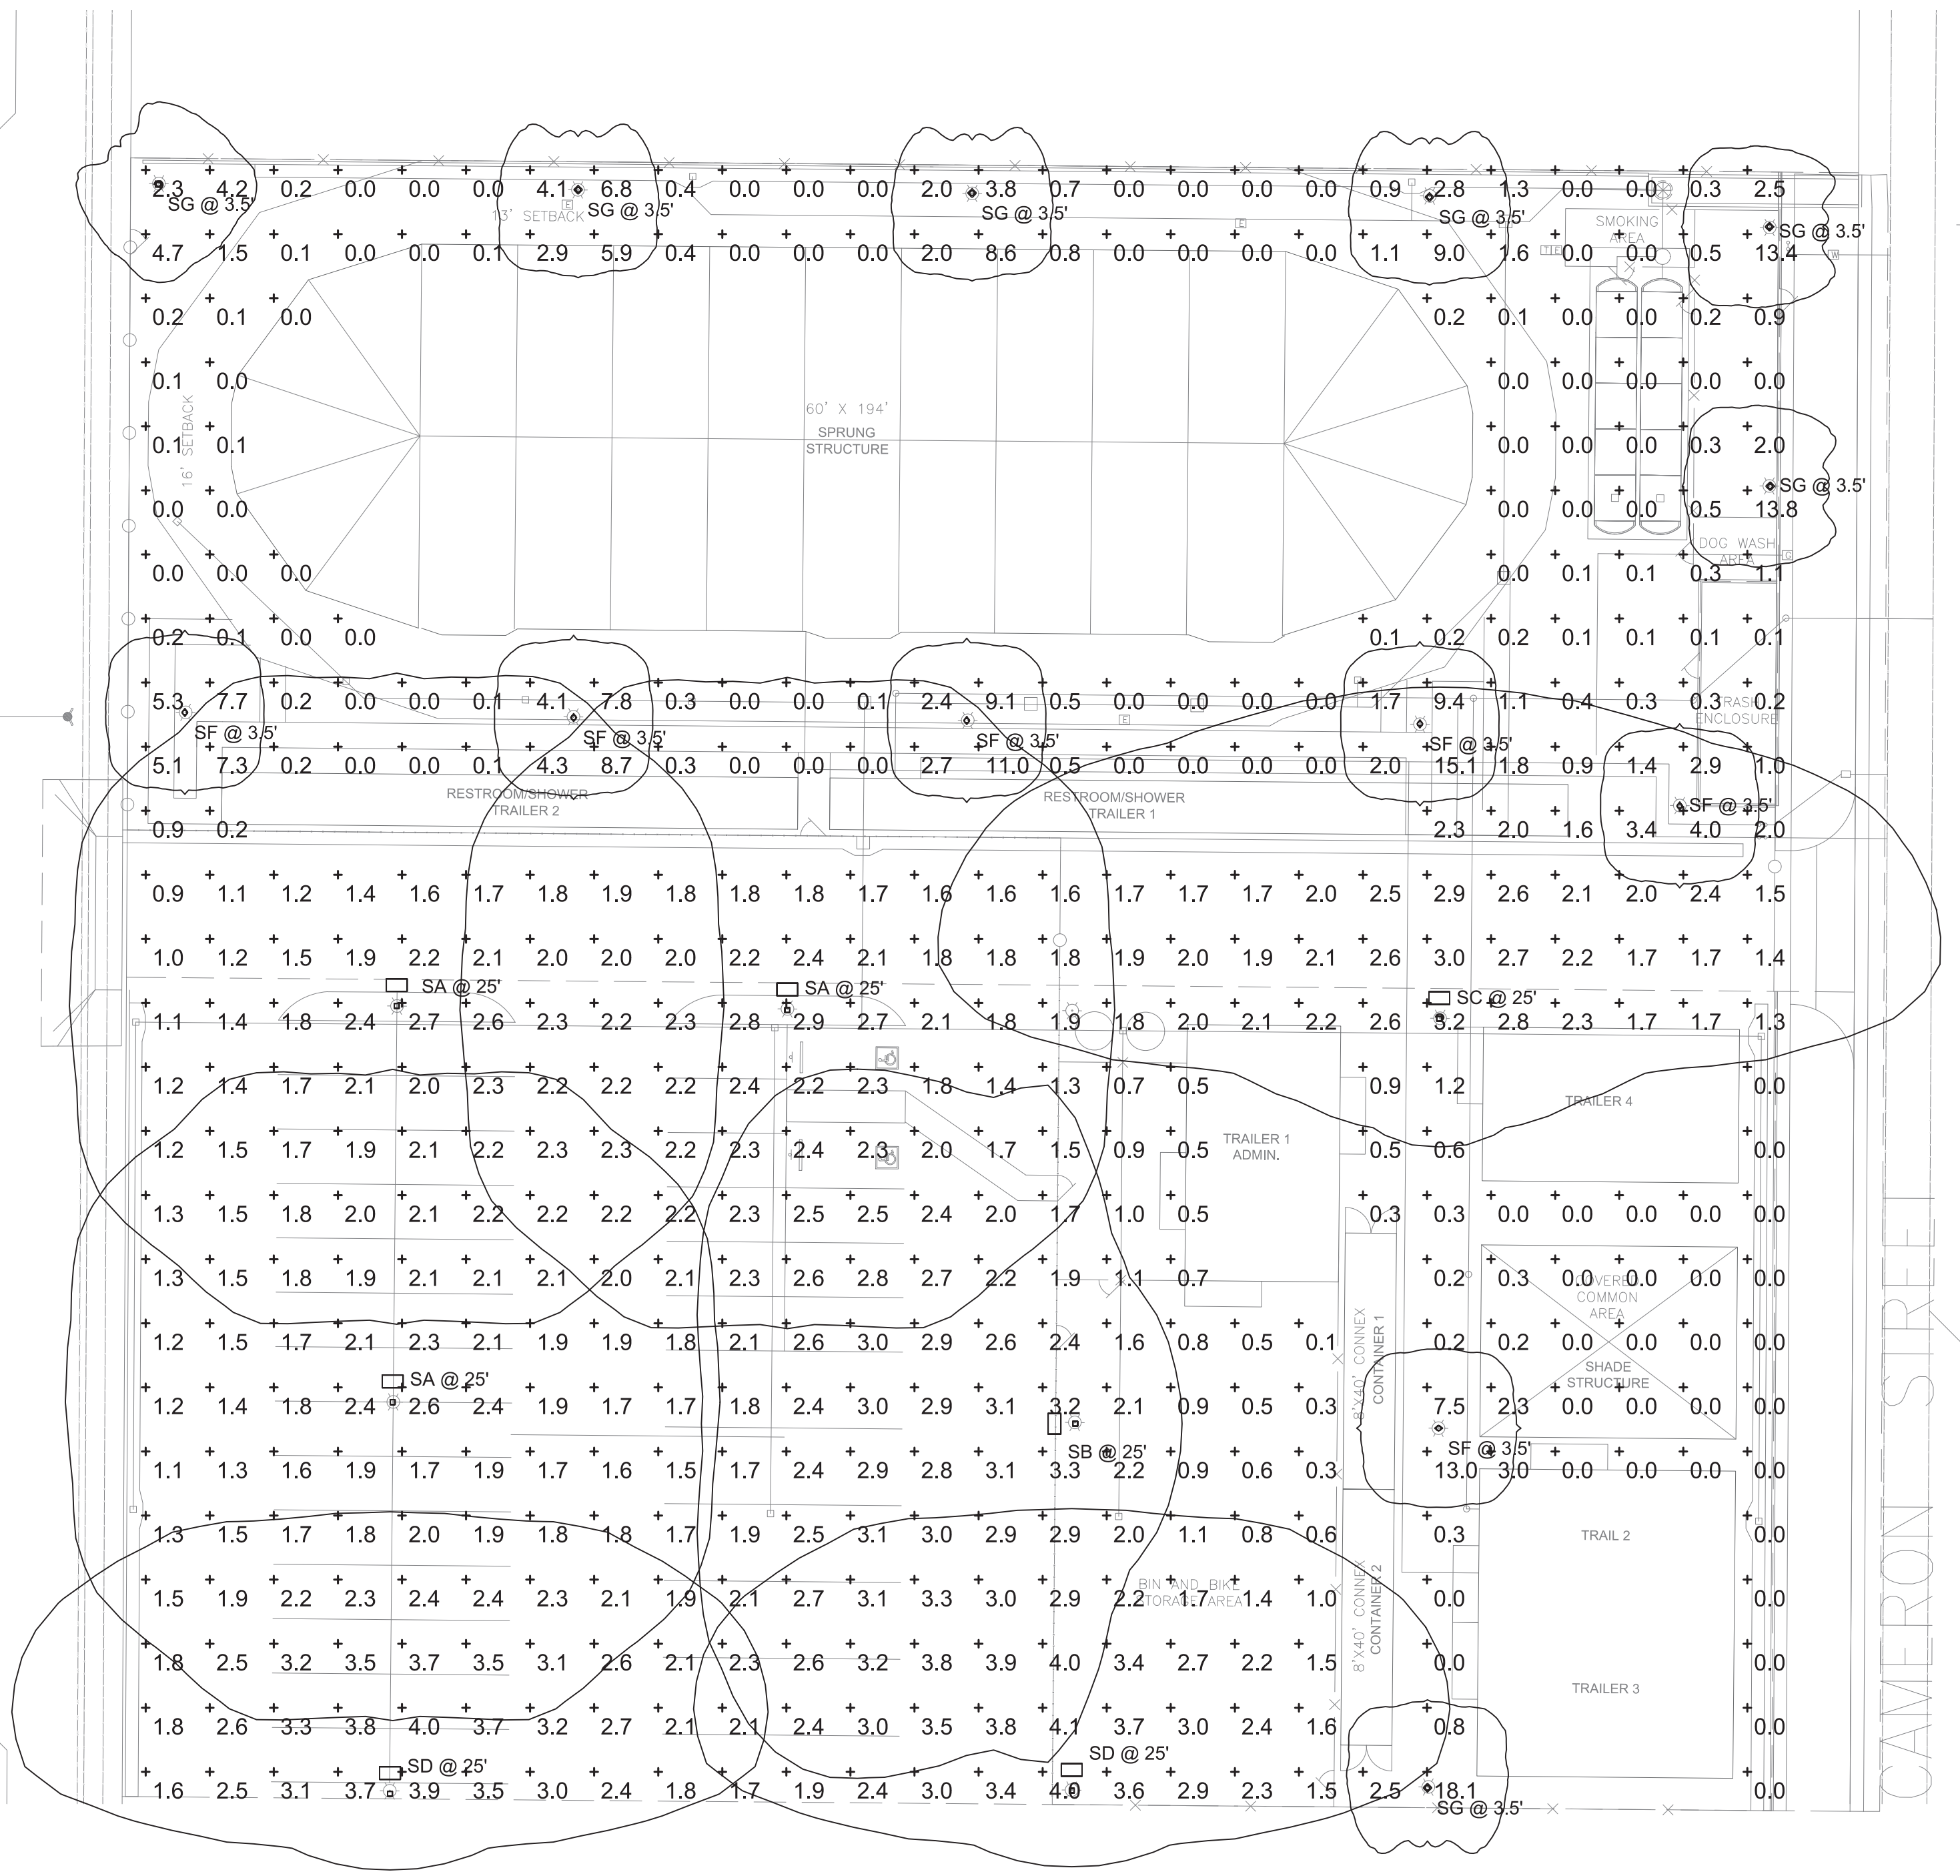

1 PHOTOMETRIC PLAN SCALE: 1"= 20'


Symbol	Label	QTY	Manufacturer	Catalog Number	Description	Lamp	Filename	Lumens per Lamp	LLF	Wattage
SA	SA	3	Lithonia Lighting	DSX0 LED P6 40K T5W MVOLT SPA (FINISH) / SSS 22.5" W/2.5" BASE	DSX0 LED P6 40K T5W MVOLT	LED	DSX0_LED_P6_40K_T5W_MVOLT.ies	16466	0.91	134
SB	SB	1	Lithonia Lighting	DSX0 LED P6 40K TFTM MVOLT SPA HS (FINISH) / SSS 22.5" W/2.5" BASE	DSX0 LED P6 40K TFTM MVOLT with houseside shield	LED	DSX0_LED_P6_40K_TFTM_MVOLT_HS.ies	12485	0.91	134
SC	SC	1	Lithonia Lighting	DSX0 LED P6 40K T2M MVOLT SPA (FINISH) / SSS 22.5" W/2.5" BASE	DSX0 LED P6 40K T2M MVOLT	LED	DSX0_LED_P6_40K_T2M_MVOLT.ies	15931	0.91	134
SD	SD	2	Lithonia Lighting	DSX0 LED P6 40K T2S MVOLT SPA HS (FINISH) / SSS 22.5" W/2.5" BASE	DSX0 LED P6 40K T2S MVOLT with houseside shield	LED	DSX0_LED_P6_40K_T2S_MVOLT_HS.ies	11015	0.91	134
SF	SF	6	Lithonia Lighting	DSXB LED 16C 700 40K SYM MVOLT (FINISH)	D-SERIES BOLLARD WITH 16 4000K LEDS OPERATED AT 700mA AND SYMMETRIC DISTRIBUTION	LED	DSXB_LED_16C_700_40K_SYM.ies	3009	0.91	39
SG	SG	7	Lithonia Lighting	DSXB LED 12C 700 40K ASY MVOLT (FINISH)	D-SERIES BOLLARD WITH 12 4000K LEDS OPERATED AT 700mA AND ASYMMETRIC DISTRIBUTION	LED	DSXB_LED_12C_700_40K_ASY.ies	2335	0.91	31

Statistics						
Description	Symbol	Avg	Max	Min	Max/Min	Avg/Min
SITE - FC @ GRADE	+	1.8 fc	18.1 fc	0.0 fc	N/A	N/A



One Lithonia Way • Cary, Georgia 30012 • Phone: 1-800-705-SERV (7378) • www.lithonia.com
© 2011-2020 Acuity Brands Lighting, Inc. All rights reserved.

DSX0 LED
Rev. 07/15/2020
Page 1 of 8

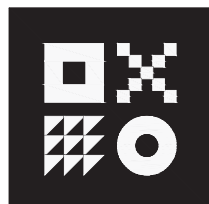

ARDEBILI
Engineering

Project Number: 20383 | Project Manager: FH
8190 E Indian School Rd. Suite 205, Scottsdale, AZ 85251
P: 480.626.7072 | ardebilieng.com



innovation | versatility | reliability

TOLL FREE: 1-800-528-9899
or (403) 601-2292 www.sprung.com




DESIGN LOADS

STRUCTURE LOCATION: HUNTINGTON BEACH, CA
BUILDING CODE: IBC 2018/CBC 2019
WIND SPEED: 106 mph 3 SEC GUST
RISK CATEGORY: II EXPOSURE C
GROUND SNOW LOAD: NA
(SEE SNOW SHED REPORT)



940 E Elm Avenue
Salt Lake City, Utah 84106
Phone: (801) 486-6848

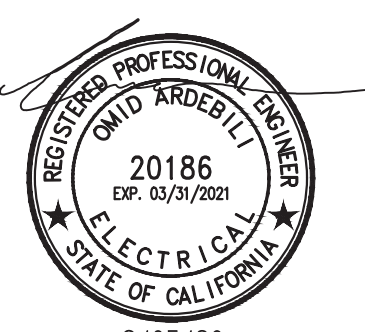

9/05/20

SIGNATURE SERIES

REV	MM/DD/YY	BY	DESCRIPTION

This drawing is protected by copyright in the United States of America, Canada and all other countries of the world. It, and all of the designs, technical data and engineering services represented by it and originated or rendered by SPRUNG INSTANT STRUCTURES INC. are the exclusive property of SPRUNG INSTANT STRUCTURES INC. and must neither be used in manufacturing nor disclosed nor reproduced in whole or in part except with the prior written consent of SPRUNG INSTANT STRUCTURES INC. Any copying of this drawing in whole or in part and any use of it to construct the subject matter illustrated in it without prior written permission of SPRUNG INSTANT STRUCTURES INC. is prohibited.

17631 CAMERON LANE
HUNTINGTON BEACH, CA 92647

PHOTOMETRIC PLAN

DRAWN BY:	DATE:
SCALE:	DRAWING #
SPRUNG WO:	E0.2

STATE OF CALIFORNIA

Indoor Lighting

NRCC-LTI-E (Created 01/20)

CALIFORNIA ENERGY COMMISSION

NRCC-LTI-E

CERTIFICATE OF COMPLIANCE

This document is used to demonstrate compliance with requirements in §110.9, §110.12(c), §130.0, §130.1, §140.6, and §141.0(b)2 for indoor lighting scopes using the prescriptive path.

Project Name: SPRUNG SHELTER

Report Page: Page 1 of 6

Project Address: HUNTING BEACH , CA

Date Prepared:

A. GENERAL INFORMATION

01 Project Location (city) HUNTING BEACH

02 Climate Zone 6

03 Occupancy Types Within Project (select all that apply):

04 Total Conditioned Floor Area (ft²) 10,737

05 Total Unconditioned Floor Area (ft²)

06 # of Stories (Habitable Above Grade) 1

☐ Office ☐ Retail ☐ Warehouse ☐ Hotel/Motel ☐ School ☐ Support Areas

☐ Parking Garage ☐ High-Rise Residential ☐ Relocatable ☐ Healthcare ☒ Other (write in): HOMELESS CENTER

B. PROJECT SCOPE

Table Instructions: Include any lighting systems that are within the scope of the permit application and are demonstrating compliance using the prescriptive path outlined in §140.6 or §141.0(b)2 for alterations. WARNING: Changing the Calculation Method in this table will result in the deletion of data previously input. If you need to change the calculation method, please open a new form or use "Save As".

Scope of Work

01

02

03

04

05

My Project Consists of (check all that apply):

Calculation Method

Area (ft²)

Calculation Method

Area (ft²)

☒ New Lighting System

☐ Altered Lighting System

Total Area of Work (ft²) 10,737

C. COMPLIANCE RESULTS

Table Instructions: If any cell on this table says "DOES NOT COMPLY" or "COMPLIES with Exceptional Conditions" refer to Table D. for guidance.

Allowed Lighting Power per §140.6(b) (Watts)

01

02

03

04

05

06

07

08

09

Lighting in conditioned and unconditioned spaces must not be combined for compliance per §140.6(b)1.

Complete Building §140.6(c)1

Area Category §140.6(c)2

Area Category Additional §140.6(c)2G (+)

Tailored §140.6(c)3 (+)

= Total Allowed (Watts)

≥ Total Designed (Watts)

Adjustments PAF Control Credits §140.6(a)2 (-)

= Total Adjusted (Watts) *Includes Adjustments

05 Must be ≥ 08 §140.6

(See Table I)

(See Table I)

(See Table J)

(See Table K)

= 4,294.8

≥ 1,544

= 1,544

COMPLIES

Conditioned:

Unconditioned:

Table Continued

CA Building Energy Efficiency Standards - 2019 Nonresidential Compliance: <http://www.energy.ca.gov/title24/2019standards>

January 2020

STATE OF CALIFORNIA

Indoor Lighting

NRCC-LTI-E (Created 01/20)

CALIFORNIA ENERGY COMMISSION

NRCC-LTI-E

CERTIFICATE OF COMPLIANCE

Project Name: SPRUNG SHELTER

Report Page: Page 2 of 6

Project Address: HUNTING BEACH , CA

Date Prepared:

Controls Compliance (See Table H for Details)

Rated Power Reduction Compliance (See Table Q for Details)

Not Applicable

D. EXCEPTIONAL CONDITIONS

This table is auto-filled with uneditable comments because of selections made or data entered in tables throughout the form.

No exceptional conditions apply to this project.

E. ADDITIONAL REMARKS

This table includes remarks made by the permit applicant to the Authority Having Jurisdiction.

F. INDOOR LIGHTING FIXTURE SCHEDULE

Table Instructions: Include all permanent designed lighting and all portable lighting in offices.

Designed Wattage: Conditioned Spaces

01

02

03

04

05

06

07

08

09

10

Name or Item Tag

Complete Luminaire Description

Modular (Track) Fixture

Small Aperture & Color Change¹

Watts per luminaire²

How Wattage is determined

Total number luminaires

Exempt per §140.6(a)3

Design Watts

Field Inspector

F/FE

4" LED STRIP

☐

☐

34

Mfr. Spec²

36

☐

1,224

Pass

Fail

P

PENDANT

☐

☐

16

Mfr. Spec²

20

☐

320

☐

☐

Total Designed Watts CONDITIONED SPACES: 1,544

G. MODULAR LIGHTING SYSTEMS

This Section Does Not Apply

CA Building Energy Efficiency Standards - 2019 Nonresidential Compliance: <http://www.energy.ca.gov/title24/2019standards>

January 2020

STATE OF CALIFORNIA

Indoor Lighting

NRCC-LTI-E (Created 01/20)

CALIFORNIA ENERGY COMMISSION

NRCC-LTI-E

CERTIFICATE OF COMPLIANCE

Project Name: SPRUNG SHELTER

Report Page: Page 3 of 6

Project Address: HUNTING BEACH , CA

Date Prepared:

H. INDOOR LIGHTING CONTROLS (Not Including PAFs)

This Section Does Not Apply

I. LIGHTING POWER ALLOWANCE: COMPLETE BUILDING OR AREA CATEGORY METHODS

Table Instructions: Complete the table for each area complying using the Complete Building or Area Category Methods per §140.6(b). Indicate if additional lighting power allowances per §140.6(c) or adjustments per §140.6(a) are being used.

Conditioned Spaces

01

02

03

04

05

06

Area Description

Complete Building or Area Category Primary Function Area

Allowed Density (W/ft²)

Area (ft²)

Allowed Wattage (Watts)

Additional Allowances / Adjustment

Area Category

PAF

HOMELESS CENTRE

All Other Space Types

0.4

10,737

4,294.8

☐

☐

TOTAL: 10,737 4,294.8

See Tables J or P for detail

J. ADDITIONAL LIGHTING ALLOWANCE: AREA CATEGORY METHOD QUALIFYING LIGHTING SYSTEM

Table Instructions: Please complete the table for all areas indicated in Table I as using an additional allowance per the Area Category Method in Table 140.6-C.

K. TAILORED METHOD GENERAL LIGHTING POWER ALLOWANCE

This Section Does Not Apply

L. ADDITIONAL LIGHTING ALLOWANCE: TAILORED WALL DISPLAY

This Section Does Not Apply

M. ADDITIONAL LIGHTING ALLOWANCE: TAILORED FLOOR AND TASK LIGHTING

This Section Does Not Apply

N. ADDITIONAL LIGHTING ALLOWANCE: TAILORED ORNAMENTAL/SPECIAL EFFECTS

This Section Does Not Apply

O. ADDITIONAL LIGHTING ALLOWANCE: TAILORED VERY VALUABLE MERCHANDISE

This Section Does Not Apply

CA Building Energy Efficiency Standards - 2019 Nonresidential Compliance: <http://www.energy.ca.gov/title24/2019standards>

January 2020

STATE OF CALIFORNIA

Indoor Lighting

NRCC-LTI-E (Created 01/20)

CALIFORNIA ENERGY COMMISSION

NRCC-LTI-E

CERTIFICATE OF COMPLIANCE

Project Name: SPRUNG SHELTER

Report Page: Page 4 of 6

Project Address: HUNTING BEACH , CA

Date Prepared:

P. POWER ADJUSTMENT: LIGHTING CONTROL CREDIT (POWER ADJUSTMENT FACTOR (PAF))

This Section Does Not Apply

Q. RATED POWER REDUCTION COMPLIANCE FOR ALTERATIONS

This Section Does Not Apply

R. 80% LIGHTING POWER FOR ALTERATIONS - CONTROLS EXCEPTIONS

This Section Does Not Apply

S. DAYLIGHT DESIGN POWER ADJUSTMENT FACTOR (PAF)

This Section Does Not Apply

T. DECLARATION OF REQUIRED CERTIFICATES OF INSTALLATION

Table Instructions: Selections have been made based on information provided in previous tables of this document. If any selection needs to be changed, please explain why in Table E. Additional Remarks. These documents must be provided to the building inspector during construction and can be found online at https://www2.energy.ca.gov/title24/2019standards/2019_compliance_documents/Nonresidential_Documents/NRCI/.

YES

NO

Form/Title

Field Inspector

Pass

Fail

☒

☐

NRCI-LTI-01-E - Must be submitted for all buildings

☐

☐

☐

☒

NRCI-LTI-02-E - Must be submitted for a lighting control system, or for an Energy Management Control System (EMCS), to be recognized for compliance.

☐

☐

☐

☒

NRCI-LTI-04-E - Must be submitted for two interlocked systems serving an auditorium, a convention center, a conference room, a multipurpose room, or a theater to be recognized for compliance.

☐

☐

☐

☒

NRCI-LTI-05-E - Must be submitted for a Power Adjustment Factor (PAF) to be recognized for compliance.

☐

☐

☐

☒

NRCI-LTI-06-E - Must be submitted for additional wattage installed in a video conferencing studio to be recognized for compliance.

☐

☐

CA Building Energy Efficiency Standards - 2019 Nonresidential Compliance: <http://www.energy.ca.gov/title24/2019standards>

January 2020

STATE OF CALIFORNIA

Indoor Lighting

NRCC-LTI-E (Created 01/20)

CALIFORNIA ENERGY COMMISSION

NRCC-LTI-E

CERTIFICATE OF COMPLIANCE

Project Name: SPRUNG SHELTER

Report Page: Page 5 of 6

Project Address: HUNTING BEACH , CA

Date Prepared:

U. DECLARATION OF REQUIRED CERTIFICATES OF ACCEPTANCE

Table Instructions: Selections have been made based on information provided in previous tables of this document. If any selection needs to be changed, please explain why in Table E. Additional Remarks. These documents must be provided to the building inspector during construction and any with "A" in the form name must be completed through an Acceptance Test Technician Certification Provider (ATTCP). For more information visit: <http://www.energy.ca.gov/title24/attcp/providers.html>

YES

NO

Form/Title

Field Inspector

Pass

Fail

☐

☒

NRCA-LTI-02-A - Must be submitted for occupancy sensors and automatic time switch controls.

☐

☐

☐

☒

NRCA-LTI-03-A - Must be submitted for automatic daylight controls.

☐

☐

☐

☒

NRCA-LTI-04-A - Must be submitted for demand responsive lighting controls.

☐

☐

☐

☒

NRCA-LTI-05-A - Must be submitted for institutional tuning power adjustment factor (PAF).

☐

☐

☐

☒

NRCA-ENV-03-F - Must be submitted for daylighting design power adjustment factors (PAF).

☐

☐

CA Building Energy Efficiency Standards - 2019 Nonresidential Compliance: <http://www.energy.ca.gov/title24/2019standards>

January 2020

STATE OF CALIFORNIA

Indoor Lighting

NRCC-LTI-E (Created 01/20)

CALIFORNIA ENERGY COMMISSION

NRCC-LTI-E

CERTIFICATE OF COMPLIANCE

Project Name: SPRUNG SHELTER

Report Page: Page 6 of 6

Project Address: HUNTING BEACH , CA

Date Prepared:

DOCUMENTATION AUTHOR'S DECLARATION STATEMENT

I certify that this Certificate of Compliance documentation is accurate and complete

Documentation Author Name: Omid Ardebili

Documentation Author Signature:

Company:

Signature Date:

Address: 8100 E. Indian School Road #205

CEA/ HERS Certification Identification (if applicable): 20186

City/State/Zip: Scottsdale, AZ 85251

Phone: 480-626-7270

RESPONSIBLE PERSON'S DECLARATION STATEMENT

I certify the following under penalty of perjury, under the laws of the State of California:

1. The information provided on this Certificate of Compliance is true and correct.

2. I am eligible under Division 3 of the Business and Professions Code to accept responsibility for the building design or system design identified on this Certificate of Compliance (responsible designer)

3. The energy features and performance specifications, materials, components, and manufactured devices for the building design or system design identified on this Certificate of Compliance conform to the requirements of Title 24, Part 1 and Part 6 of the California Code of Regulations.

4. The building design features or system design features identified on this Certificate of Compliance are consistent with the information provided on other applicable compliance documents, worksheets, calculations, plans and specifications submitted to the enforcement agency for approval with this building permit application.

5. I will ensure that a completed signed copy of this Certificate of Compliance shall be made available with the building permit(s) issued for the building, and made available to the enforcement agency for all applicable inspections. I understand that a completed signed copy of this Certificate of Compliance is required to be included with the documentation the builder provides to the building owner at occupancy.

Responsible Designer Name: Omid Ardebili

Responsible Designer Signature:

Company :

Date Signed:

Address: 8100 E. Indian School Road #205


License: 20186

City/State/Zip: Scottsdale, AZ 85251

Phone: 480-626-7270

CA Building Energy Efficiency Standards - 2019 Nonresidential Compliance: <http://www.energy.ca.gov/title24/2019standards>

January 2020

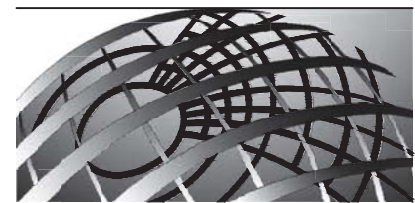

innovation | versatility | reliability

TOLL FREE: 1-800-528-9899
or (403) 601-2292 www.sprung.com



DESIGN LOADS

STRUCTURE LOCATION:HUNTINGTON BEACH, CA
BUILDING CODE: IBC 2018/CBC 2019
WIND SPEED: 106 mph 3 SEC GUST
RISK CATEGORY: II EXPOSURE C
GROUND SNOW LOAD: NA
(SEE SNOW SHED REPORT)



940 E Elm Avenue
Salt Lake City, Utah 84106
Phone: (801) 486-6848



SIGNATURE SERIES


REV	MM/DD/YY	BY	DESCRIPTION

This drawing is protected by copyright in the United States of America, Canada and all other countries of the world. It, and all of the designs, technical data and engineering services represented by it and originated or rendered by SPRUNG INSTANT STRUCTURES INC. are the exclusive property of SPRUNG INSTANT STRUCTURES INC. and must neither be used in manufacturing nor disclosed nor reproduced in whole or in part except with the prior written consent of SPRUNG INSTANT STRUCTURES INC. Any copying of this drawing in whole or in part and any use of it to construct the subject matter illustrated in it without prior written permission of SPRUNG INSTANT STRUCTURES INC. is prohibited.

17631 CAMERON LANE
HUNTINGTON BEACH, CA 92647

INTERIOR TITLE 24

DRAWN BY:	DATE:
SCALE:	DRAWING #
SPRUNG WO:	E0.3

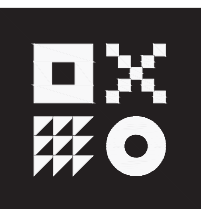

ARDEBILI
Engineering

Project Number: 20383 | Project Manager: FH
8100 E Indian School Rd. Suite 205, Scottsdale, AZ 85251
P: 480.626.7072 | ardebilieng.com

DRAWN BY:	DATE:
SCALE:	DRAWING #
SPRUNG WO:	E0.3

STATE OF CALIFORNIA
Outdoor Lighting

CERTIFICATE OF COMPLIANCE

Project Name: SPRUNG SHELTER
Project Address: HUNTING BEACH, CA

Report Page: Page 1 of 7
Date Prepared:

A. GENERAL INFORMATION

01 Project Location (city)

HUNTING BEACH

04 Total Illuminated Hardscape Area (ft²)

31,598

02 Climate Zone

6

03 Outdoor Lighting Zone per Title 24, Part 1 §10-11.4 or as designated by Authority Having Jurisdiction (AHJ):

LZ-0: Very Low - Undeveloped Parkland

LZ-2: Moderate - Rural Areas

LZ-4: High - Must be reviewed by CA Energy Commission for Approval

☐

☒

☐

LZ-1: Low - Developed Parkland

LZ-3: Moderately High - Urban Areas

B. PROJECT SCOPE

Table Instructions: Include any outdoor lighting systems that are within the scope of the permit application and are demonstrating compliance using the prescriptive path outlined in §140.2 or §141.0(b)(2), for alterations.
My project consists of:

☒ New Lighting System

☐ Altered Lighting System

01

02

Must Comply with Allowances from §140.2.

Is your alteration increasing the connected lighting load (Watts)?

☐ Yes

☐ No

03

04

05

% of Existing Luminaires Being Altered¹

Sum Total of Luminaires Being Added or Altered

Calculation Method

¹ FOOTNOTES: % of Existing Luminaires Being Altered = (Sum Total of Luminaires Being Added or Altered / Existing Luminaires within the Scope of the Permit Application) x 100

C. COMPLIANCE RESULTS

Table Instructions: If any cell on this table says "DOES NOT COMPLY" or "COMPLIES with Exceptional Conditions" refer to Table D, for guidance.

Calculation of Total Allowed Lighting Power (Watts) §140.7 or §141.0(b)(2)L

Compliance Results

01

02

03

04

05

06

07

08

09

General Hardscape Allowance §140.7(d)(1)
(See Table I)

Per Application §140.7(d)(2)
(See Table J)

Sales Frontage §140.7(d)(2)
(See Table K)

Ornamental §140.7(d)(2)
(See Table L)

Per Specific Area §140.7(d)(2)
(See Table M)

Existing Power §141.0(b)(2)L
(See Table N)

=

Total Allowed (Watts)

≥

Total Actual (Watts)

07 Must be ≥ 08

1,164.95

+

+

+

+

296

OR

=

1,460.95

≥

1,389

COMPLIES

Cutoff Compliance (See Table G for Details)

Not Applicable

COMPLIES

Controls Compliance (See Table H for Details)

COMPLIES

CA Building Energy Efficiency Standards - 2019 Nonresidential Compliance: <http://www.energy.ca.gov/title24/2019standards> November 2019

STATE OF CALIFORNIA
Outdoor Lighting

CERTIFICATE OF COMPLIANCE

Project Name: SPRUNG SHELTER
Project Address: HUNTING BEACH, CA

Report Page: Page 4 of 7
Date Prepared:

Table Continued

01

General Hardscape Allowance

"Use it or lose it" Allowances (select all that apply)

☒ Per Application

☐ Sales Frontage

☐ Ornamental

☒ Per Specific Area

Table I (below)

Table J

Table K

Table L

Table M

Calculated General Hardscape Lighting Power Allowance per Table 140.7-A (LZ 2 & 3)

02

03

04

05

06

07

08

09

10

Area Description

Surface Type

Illuminated Area (ft²)

Area Wattage Allowance (AWA) (W/ft²)

Area Allowance (Watts)

Perimeter Length (lf)

Allowed Density (W/lf)

Linear Wattage Allowance (LWA) (Watts)

Total General AWA + LWA (Watts)

PARKING LOT

Asphalt

31,598

0.025

789.95

100

0.25

25

814.95

Initial Wattage Allowance for Entire Site (Watts):

350

Total General Hardscape Allowance (Watts):

1,164.95

J. LIGHTING ALLOWANCE: PER APPLICATION

This Section Does Not Apply

K. LIGHTING ALLOWANCE: SALES FRONTAGE

This Section Does Not Apply

L. LIGHTING ALLOWANCE: ORNAMENTAL

This Section Does Not Apply

M. LIGHTING ALLOWANCE: PER SPECIFIC AREA

Table Instructions: Please complete this table for areas using the wattage allowance per specific area type from Table 140.7-B. More than one specific area allowance may be taken in a single project, if applicable. However, multiple specific area allowances may not be taken for the exact same area on the site.
Table Continued

CA Building Energy Efficiency Standards - 2019 Nonresidential Compliance: <http://www.energy.ca.gov/title24/2019standards> November 2019

STATE OF CALIFORNIA
Outdoor Lighting

CERTIFICATE OF COMPLIANCE

Project Name: SPRUNG SHELTER
Project Address: HUNTING BEACH, CA

Report Page: Page 7 of 7
Date Prepared:

DOCUMENTATION AUTHOR'S DECLARATION STATEMENT

I certify that this Certificate of Compliance documentation is accurate and complete

Documentation Author Name: Omid Ardebili

Documentation Author Signature:

Company: Signature Date: 2020.07.31

Address: 8100 E. Indian School Road CEA/ HERS Certification Identification (if applicable): 20186

City/State/Zip: Scottsdale, AZ 85251 Phone: 480-626-7270

RESPONSIBLE PERSON'S DECLARATION STATEMENT

I certify the following under penalty of perjury, under the laws of the State of California:

1. The information provided on this Certificate of Compliance is true and correct.

2. I am eligible under Division 3 of the Business and Professions Code to accept responsibility for the building design or system design identified on this Certificate of Compliance (responsible designer).

3. The energy features and performance specifications, materials, components, and manufactured devices for the building design or system design identified on this Certificate of Compliance conform to the requirements of Title 24, Part 1 and Part 6 of the California Code of Regulations.

4. The building design features or system design features identified on this Certificate of Compliance are consistent with the information provided on other applicable compliance documents, worksheets, calculations, plans and specifications submitted to the enforcement agency for approval with this building permit application.

5. I will ensure that a completed signed copy of this Certificate of Compliance shall be made available with the building permit(s) issued for the building, and made available to the enforcement agency for all applicable inspections. I understand that a completed signed copy of this Certificate of Compliance is required to be included with the documentation the builder provides to the building owner at occupancy.

Responsible Designer Name: Omid Ardebili

Responsible Designer Signature:

Company: Date Signed: 2020.07.31

Address: 8100 E. Indian School Road License: 20186

City/State/Zip: Scottsdale, AZ 85251 Phone: 480-626-7270

CA Building Energy Efficiency Standards - 2019 Nonresidential Compliance: <http://www.energy.ca.gov/title24/2019standards> November 2019

STATE OF CALIFORNIA
Outdoor Lighting

CERTIFICATE OF COMPLIANCE

Project Name: SPRUNG SHELTER
Project Address: HUNTING BEACH, CA

Report Page: Page 2 of 7
Date Prepared:

D. EXCEPTIONAL CONDITIONS

This table is auto-filled with uneditable comments because of selections made or data entered in tables throughout the form.

No exceptional conditions apply to this project.

E. ADDITIONAL REMARKS

This table includes remarks made by the permit applicant to the Authority Having Jurisdiction.

F. OUTDOOR LIGHTING FIXTURE SCHEDULE

Table Instructions: For new or altered lighting systems demonstrating compliance with §140.7 (ie Table I has expanded for input), include all luminaires being installed and any existing luminaires remaining or being moved within the spaces covered by the permit application in the Table below. For altered lighting systems using the Existing Power method per §141.0(b)(2) (ie Table N has expanded for input), include only new luminaires being installed and replacement luminaires being installed as part of the project scope (ie, do not include existing luminaires remaining or existing luminaires being moved).

Designed Wattage:

01

02

03

04

05

06

07

08

09

10

Name or Item Tag

Complete Luminaire Description

Watts per luminaire¹²

How Wattage is determined

Total number luminaires³

Luminaire Status³

Excluded per §140.7(a)

Design Watts

Cutoff Req. ≥ 6,200 initial lumen output §130.2(b)⁴

Field Inspector

SF

LED

☐ Linear

39

Mfr. Spec¹

6

New

☐

234

NA: <6,200 lumens

☐

☐

SG

LED

☐ Linear

31

Mfr. Spec¹

7

New

☐

217

NA: <6,200 lumens

☐

☐

SA/SB

POLE

☐ Linear

134

Mfr. Spec¹

4

New

☐

536

NA: <6,200 lumens

☐

☐

SC/SD

POLE

☐ Linear

134

Mfr. Spec¹

3

New

☐

402

NA: <6,200 lumens

☐

☐

Total Designed Watts:

1,389

¹ NOTES: Selections with a * require a note in the space below explaining how compliance is achieved.
EX: Luminaire is lighting a statue; EXCEPTION 2 to §130.2(b).

CA Building Energy Efficiency Standards - 2019 Nonresidential Compliance: <http://www.energy.ca.gov/title24/2019standards> November 2019

STATE OF CALIFORNIA
Outdoor Lighting

CERTIFICATE OF COMPLIANCE

Project Name: SPRUNG SHELTER
Project Address: HUNTING BEACH, CA

Report Page: Page 5 of 7
Date Prepared:

01

02

03

04

05

06

07

08

09

10

Area Description

Specific Area Type per Table 140.7-B

CALCULATED ALLOWANCE (Watts)
Specific Area (ft²)²

Allowed Density (W/ft²)

Extra Allowance (Watts)

Luminaire Name or Item Tag

Watts per Luminaire²

of Luminaires³

Design Watts

Additional Allowance (Watts)

BUILDING

Outdoor Sales Lot

214,855

0.28

60,159.4

SF

39

6

234

SG

31

2

62

Total Design Watts for this Area:

296

296

Total Allowance (Watts) All Areas:

296

¹ FOOTNOTES: See Table 140.7-B for the rules for calculating the specific areas (ft²) for these additional lighting allowances.
² For luminaires indicated in Table F as linear, wattage in column 07 is W/lf instead of Watts/luminaire. Total linear feet for the luminaire should be indicated in column 08 instead of number of luminaires.

N. EXISTING CONDITIONS POWER ALLOWANCE (alterations only)

This Section Does Not Apply

O. DECLARATION OF REQUIRED CERTIFICATES OF INSTALLATION

Table Instructions: Selections have been made based on information provided in previous tables of this document. If any selection needs to be changed, please explain why in Table E. Additional Remarks. These documents must be provided to the building inspector during construction and can be found online at https://www.energy.ca.gov/title24/2019standards/2019_compliance_documents/Nonresidential_Documents/NRCL.

YES

NO

Form/Title

Field Inspector

☒

☐

NRCL-LTO-01-E - Must be submitted for all buildings.

☐

☐

☒

☐

NRCL-LTO-02-E - Must be submitted for a lighting control system; or for an Energy Management Control System (EMCS), to be recognized for compliance.

☐

☐

CA Building Energy Efficiency Standards - 2019 Nonresidential Compliance: <http://www.energy.ca.gov/title24/2019standards> November 2019

STATE OF CALIFORNIA
Outdoor Lighting

CERTIFICATE OF COMPLIANCE

Project Name: SPRUNG SHELTER
Project Address: HUNTING BEACH, CA

Report Page: Page 3 of 7
Date Prepared:

¹ FOOTNOTES: Authority Having Jurisdiction may ask for Luminaire cut sheets to confirm wattage used for compliance per §130.0(c)
² For linear luminaires, wattage should be indicated as W/lf instead of Watts/luminaire. Total linear feet for the luminaire should be indicated in column 05 instead of number of luminaires.
³ Select "New" for new luminaires in a new outdoor lighting project or for added luminaires in an alteration. Select "Altered" for replacement luminaires in an alteration. Select "Existing to Remain" for existing luminaires within the project scope that are not being altered and are remaining. Select "Existing Reinstalled" for existing luminaires which are being removed and reinstalled as part of the project scope
⁴ Compliance with mandatory cutoff requirements is required for luminaires with initial lumen output ≥ 6,200 unless exempted by §130.2(b).

G. CUTOFF REQUIREMENTS (BUG)

This Section Does Not Apply

H. OUTDOOR LIGHTING CONTROLS

Table Instructions: Complete this table demonstrating compliance with controls requirements for all new or altered luminaires installed as part of the permit application. For alteration projects, luminaires which are existing to remain (ie untouched) and luminaires which are removed and reinstalled (wiring only) do not need to be included in this table even if they are within the spaces covered by the permit application.
When an option having a * is selected, the notes section of this table must be completed. The lighting controls section of the Compliance Summary Table on the first page will show "DOES NOT COMPLY" if the notes are left blank. For each requirement in columns 02 through 04, do not leave the field blank, instead select NA or Exempt* from the dropdown list to indicate not applicable or an exemption.

Mandatory Controls

01

02

03

04

05

Area Description

Shut-Off §130.2(c)(1)

Auto-Schedule §130.2(c)(2)

Motion Sensor §130.2(c)(3)

Field Inspector

BUILDING LIGHTING

Photocontrol

Yes

NA: Wall ≤ 24ft

☐

☐

PARKING LOT

Photocontrol

Yes

NA: Façade, etc. ≤ 24ft

☐

☐

*NOTES: Controls with a * require a note in the space below explaining how compliance is achieved.
EX: Not permitted by health & safety to be turned off; EXCEPTION 1 to §130.2(c).

I. LIGHTING POWER ALLOWANCE (per §140.7)

Table Continued

CA Building Energy Efficiency Standards - 2019 Nonresidential Compliance: <http://www.energy.ca.gov/title24/2019standards> November 2019

STATE OF CALIFORNIA
Outdoor Lighting

CERTIFICATE OF COMPLIANCE

Project Name: SPRUNG SHELTER
Project Address: HUNTING BEACH, CA

Report Page: Page 6 of 7
Date Prepared:

P. DECLARATION OF REQUIRED CERTIFICATES OF ACCEPTANCE

Table Instructions: Selections have been made based on information provided in previous tables of this document. If any selection needs to be changed, please explain why in Table E. Additional Remarks. These documents must be provided to the building inspector during construction and must be completed through an Acceptance Test Technician Certification Provider (ATTCP). For more information visit: <http://www.energy.ca.gov/title24/atcp/providers.html>

YES

NO

Form/Title

Field Inspector

☒

☐

NRCA-LTO-02-A - Must be submitted for all outdoor lighting controls except for alterations where controls area added to ≤ 20 luminaires.

☐

☐

CA Building Energy Efficiency Standards - 2019 Nonresidential Compliance: <http://www.energy.ca.gov/title24/2019standards> November 2019

STATE OF CALIFORNIA
Outdoor Lighting

CERTIFICATE OF COMPLIANCE

Project Name: SPRUNG SHELTER
Project Address: HUNTING BEACH, CA

Report Page: Page 7 of 7
Date Prepared:

DOCUMENTATION AUTHOR'S DECLARATION STATEMENT

I certify that this Certificate of Compliance documentation is accurate and complete

Documentation Author Name: Omid Ardebili

Documentation Author Signature:

Company: Signature Date: 2020.07.31

Address: 8100 E. Indian School Road CEA/ HERS Certification Identification (if applicable): 20186

City/State/Zip: Scottsdale, AZ 85251 Phone: 480-626-7270

RESPONSIBLE PERSON'S DECLARATION STATEMENT

I certify the following under penalty of perjury, under the laws of the State of California:

1. The information provided on this Certificate of Compliance is true and correct.

2. I am eligible under Division 3 of the Business and Professions Code to accept responsibility for the building design or system design identified on this Certificate of Compliance (responsible designer).

3. The energy features and performance specifications, materials, components, and manufactured devices for the building design or system design identified on this Certificate of Compliance conform to the requirements of Title 24, Part 1 and Part 6 of the California Code of Regulations.

4. The building design features or system design features identified on this Certificate of Compliance are consistent with the information provided on other applicable compliance documents, worksheets, calculations, plans and specifications submitted to the enforcement agency for approval with this building permit application.

5. I will ensure that a completed signed copy of this Certificate of Compliance shall be made available with the building permit(s) issued for the building, and made available to the enforcement agency for all applicable inspections. I understand that a completed signed copy of this Certificate of Compliance is required to be included with the documentation the builder provides to the building owner at occupancy.

Responsible Designer Name: Omid Ardebili

Responsible Designer Signature:

Company: Date Signed: 2020.07.31

Address: 8100 E. Indian School Road License: 20186

City/State/Zip: Scottsdale, AZ 85251 Phone: 480-626-7270

CA Building Energy Efficiency Standards - 2019 Nonresidential Compliance: <http://www.energy.ca.gov/title24/2019standards> November 2019

STATE OF CALIFORNIA
Outdoor Lighting

CERTIFICATE OF COMPLIANCE

Project Name: SPRUNG SHELTER
Project Address: HUNTING BEACH, CA

Report Page: Page 2 of 7
Date Prepared:

D. EXCEPTIONAL CONDITIONS

This table is auto-filled with uneditable comments because of selections made or data entered in tables throughout the form.

No exceptional conditions apply to this project.

E. ADDITIONAL REMARKS

This table includes remarks made by the permit applicant to the Authority Having Jurisdiction.

F. OUTDOOR LIGHTING FIXTURE SCHEDULE

Table Instructions: For new or altered lighting systems demonstrating compliance with §140.7 (ie Table I has expanded for input), include all luminaires being installed and any existing luminaires remaining or being moved within the spaces covered by the permit application in the Table below. For altered lighting systems using the Existing Power method per §141.0(b)(2) (ie Table N has expanded for input), include only new luminaires being installed and replacement luminaires being installed as part of the project scope (ie, do not include existing luminaires remaining or existing luminaires being moved).

Designed Wattage:

01

02

03

04

05

06

07

08

09

10

Name or Item Tag

Complete Luminaire Description

Watts per luminaire¹²

How Wattage is determined

Total number luminaires³

Luminaire Status³

Excluded per §140.7(a)

Design Watts

Cutoff Req. ≥ 6,200 initial lumen output §130.2(b)⁴

Field Inspector

SF

LED

☐ Linear

39

Mfr. Spec¹

6

New

☐

234

NA: <6,200 lumens

☐

☐

SG

LED

☐ Linear

31

Mfr. Spec¹

7

New

☐

217

NA: <6,200 lumens

☐

☐

SA/SB

POLE

☐ Linear

134

Mfr. Spec¹

4

New

☐

536

NA: <6,200 lumens

☐

☐

SC/SD

POLE

☐ Linear

134

Mfr. Spec¹

3

New

☐

402

NA: <6,200 lumens

☐

☐

Total Designed Watts:

1,389

¹ NOTES: Selections with a * require a note in the space below explaining how compliance is achieved.
EX: Luminaire is lighting a statue; EXCEPTION 2 to §130.2(b).

CA Building Energy Efficiency Standards - 2019 Nonresidential Compliance: <http://www.energy.ca.gov/title24/2019standards> November 2019

STATE OF CALIFORNIA
Outdoor Lighting

CERTIFICATE OF COMPLIANCE

Project Name: SPRUNG SHELTER
Project Address: HUNTING BEACH, CA

Report Page: Page 3 of 7
Date Prepared:

D. EXCEPTIONAL CONDITIONS

This table is auto-filled with uneditable comments because of selections made or data entered in tables throughout the form.

No exceptional conditions apply to this project.

E. ADDITIONAL REMARKS

This table includes remarks made by the permit applicant to the Authority Having Jurisdiction.

F. OUTDOOR LIGHTING FIXTURE SCHEDULE

Table Instructions: For new or altered lighting systems demonstrating compliance with §140.7 (ie Table I has expanded for input), include all luminaires being installed and any existing luminaires remaining or being moved within the spaces covered by the permit application in the Table below. For altered lighting systems using the Existing Power method per §141.0(b)(2) (ie Table N has expanded for input), include only new luminaires being installed and replacement luminaires being installed as part of the project scope (ie, do not include existing luminaires remaining or existing luminaires being moved).

Designed Wattage:

01

02

03

04

05

06

07

08

09

10

Name or Item Tag

Complete Luminaire Description

Watts per luminaire¹²

How Wattage is determined

Total number luminaires³

Luminaire Status³

Excluded per §140.7(a)

Design Watts

Cutoff Req. ≥ 6,200 initial lumen output §130.2(b)⁴

Field Inspector

SF

LED

☐ Linear

39

Mfr. Spec¹

6

New

☐

234

NA: <6,200 lumens

☐

☐

SG

LED

☐ Linear

31

Mfr. Spec¹

7

New

☐

217

NA: <6,200 lumens

☐

☐

SA/SB

POLE

☐ Linear

134

Mfr. Spec¹

4

New

☐

536

NA: <6,200 lumens

☐

☐

SC/SD

POLE

☐ Linear

134

Mfr. Spec¹

3

New

☐

402

NA: <6,200 lumens

☐

☐

Total Designed Watts:

1,389

¹ NOTES: Selections with a * require a note in the space below explaining how compliance is achieved.
EX: Luminaire is lighting a statue; EXCEPTION 2 to §130.2(b).

CA Building Energy Efficiency Standards - 2019 Nonresidential Compliance: <http://www.energy.ca.gov/title24/2019standards> November 2019STATE OF CALIFORNIA
Outdoor Lighting

CERTIFICATE OF COMPLIANCE

Project Name: SPRUNG SHELTER
Project Address: HUNTING BEACH, CAReport Page: Page 4 of 7
Date Prepared:

D. EXCEPTIONAL CONDITIONS

This table is auto-filled with uneditable comments because of selections made or data entered in tables throughout the form.

No exceptional conditions apply to this project.

E. ADDITIONAL REMARKS

This table includes remarks made by the permit applicant to the Authority Having Jurisdiction.

F. OUTDOOR LIGHTING FIXTURE SCHEDULE

Table Instructions: For new or altered lighting systems demonstrating compliance with §140.7 (ie Table I has expanded for input), include all luminaires being installed and any existing luminaires remaining or being moved within the spaces covered by the permit application in the Table below. For altered lighting systems using the Existing Power method per §141.0(b)(2) (ie Table N has expanded for input), include only new luminaires being installed and replacement luminaires being installed as part of the project scope (ie, do not include existing luminaires remaining or existing luminaires being moved).

Designed Wattage:

01

02

03

04

05

06

07

08

09

10

Name or Item Tag

Complete Luminaire Description

Watts per luminaire¹²

How Wattage is determined

Total number luminaires³

Luminaire Status³

Excluded per §140.7(a)

Design Watts

Cutoff Req. ≥ 6,200 initial lumen output §130.2(b)⁴

Field Inspector

SF

LED

☐ Linear

39

Mfr. Spec¹

6

New

☐

234

NA: <6,200 lumens

☐

☐

SG

LED

☐ Linear

31

Mfr. Spec¹

7

New

☐

217

NA: <6,200 lumens

☐

☐

SA/SB

POLE

☐ Linear

134

Mfr. Spec¹

4

New

☐

536

NA: <6,200 lumens

☐

☐

SC/SD

POLE

☐ Linear

134

Mfr. Spec¹

3

New

☐

402

NA: <6,200 lumens

☐

☐

Total Designed Watts:

1,389

¹ NOTES: Selections with a * require a note in the space below explaining how compliance is achieved.
EX: Luminaire is lighting a statue; EXCEPTION 2 to §130.2(b).

CA Building Energy Efficiency Standards - 2019 Nonresidential Compliance: <http://www.energy.ca.gov/title24/2019standards> November 2019STATE OF CALIFORNIA
Outdoor Lighting

CERTIFICATE OF COMPLIANCE

Project Name: SPRUNG SHELTER
Project Address: HUNTING BEACH, CAReport Page: Page 5 of 7
Date Prepared:

D. EXCEPTIONAL CONDITIONS

This table is auto-filled with uneditable comments because of selections made or data entered in tables throughout the form.

No exceptional conditions apply to this project.

E. ADDITIONAL REMARKS

This table includes remarks made by the permit applicant to the Authority Having Jurisdiction.

F. OUTDOOR LIGHTING FIXTURE SCHEDULE

Table Instructions: For new or altered lighting systems demonstrating compliance with §140.7 (ie Table I has expanded for input), include all luminaires being installed and any existing luminaires remaining or being moved within the spaces covered by the permit application in the Table below. For altered lighting systems using the Existing Power method per §141.0(b)(2) (ie Table N has expanded for input), include only new luminaires being installed and replacement luminaires being installed as part of the project scope (ie, do not include existing luminaires remaining or existing luminaires being moved).

Designed Wattage:

01

02

03

04

05

06

07

08

09

10

Name or Item Tag

Complete Luminaire Description

Watts per luminaire¹²

How Wattage is determined

Total number luminaires³

Luminaire Status³

Excluded per §140.7(a)

Design Watts

Cutoff Req. ≥ 6,200 initial lumen output §130.2(b)⁴

Field Inspector

SF

LED

☐ Linear

39

Mfr. Spec¹

6

New

☐

234

NA: <6,200 lumens

☐

☐

SG

LED

☐ Linear

31

Mfr. Spec¹

7

New

☐

217

NA: <6,200 lumens

☐

☐

SA/SB

POLE

☐ Linear

134

Mfr. Spec¹

4

New

☐

536

NA: <6,200 lumens

☐

☐

SC/SD

POLE

☐ Linear

134

Mfr. Spec¹

3

New

☐

402

NA: <6,200 lumens

☐

☐

Total Designed Watts:

1,389

¹ NOTES: Selections with a * require a note in the space below explaining how compliance is achieved.
EX: Luminaire is lighting a statue; EXCEPTION 2 to §130.2(b).

CA Building Energy Efficiency Standards - 2019 Nonresidential Compliance: <http://www.energy.ca.gov/title24/2019standards> November 2019STATE OF CALIFORNIA
Outdoor Lighting

CERTIFICATE OF COMPLIANCE

Project Name: SPRUNG SHELTER
Project Address: HUNTING BEACH, CAReport Page: Page 6 of 7
Date Prepared:

D. EXCEPTIONAL CONDITIONS

This table is auto-filled with uneditable comments because of selections made or data entered in tables throughout the form.

No exceptional conditions apply to this project.

E. ADDITIONAL REMARKS

This table includes remarks made by the permit applicant to the Authority Having Jurisdiction.

F. OUTDOOR LIGHTING FIXTURE SCHEDULE

Table Instructions: For new or altered lighting systems demonstrating compliance with §140.7 (ie Table I has expanded for input), include all luminaires being installed and any existing luminaires remaining or being moved within the spaces covered by the permit application in the Table below. For altered lighting systems using the Existing Power method per §141.0(b)(2) (ie Table N has expanded for input), include only new luminaires being installed and replacement luminaires being installed as part of the project scope (ie, do not include existing luminaires remaining or existing luminaires being moved).

Designed Wattage:

01

02

03

04

05

06

07

08

09

10

Name or Item Tag

Complete Luminaire Description

Watts per luminaire¹²

How Wattage is determined

Total number luminaires³

Luminaire Status³

Excluded per §140.7(a)

Design Watts

Cutoff Req. ≥ 6,200 initial lumen output §130.2(b)⁴

Field Inspector

SF

LED

☐ Linear

39

Mfr. Spec¹

6

New

☐

234

NA: <6,200 lumens

☐

☐

SG

LED

☐ Linear

31

Mfr. Spec¹

7

New

☐

217

NA: <6,200 lumens

☐

☐

SA/SB

POLE

☐ Linear

134

Mfr. Spec¹

4

New

☐

536

NA: <6,200 lumens

☐

☐

SC/SD

POLE

☐ Linear

134

Mfr. Spec¹

3

New

☐

402

NA: <6,200 lumens

☐

☐

Total Designed Watts:

1,389

¹ NOTES: Selections with a * require a note in the space below explaining how compliance is achieved.
EX: Luminaire is lighting a statue; EXCEPTION 2 to §130.2(b).

CA Building Energy Efficiency Standards - 2019 Nonresidential Compliance: <http://www.energy.ca.gov/title24/2019standards> November 2019STATE OF CALIFORNIA
Outdoor Lighting

CERTIFICATE OF COMPLIANCE

Project Name: SPRUNG SHELTER
Project Address: HUNTING BEACH, CAReport Page: Page 7 of 7
Date Prepared:

D. EXCEPTIONAL CONDITIONS

This table is auto-filled with uneditable comments because of selections made or data entered in tables throughout the form.


No exceptional conditions apply to this project.


E. ADDITIONAL REMARKS

This table includes remarks made by the permit applicant to the Authority Having Jurisdiction.

F. OUTDOOR LIGHTING FIXTURE SCHEDULE

Table Instructions: For new or altered lighting systems demonstrating compliance with §140.7 (ie Table I has expanded for input), include all luminaires being installed and any existing luminaires remaining or being moved within the spaces covered by the permit application in the Table below. For altered lighting systems using

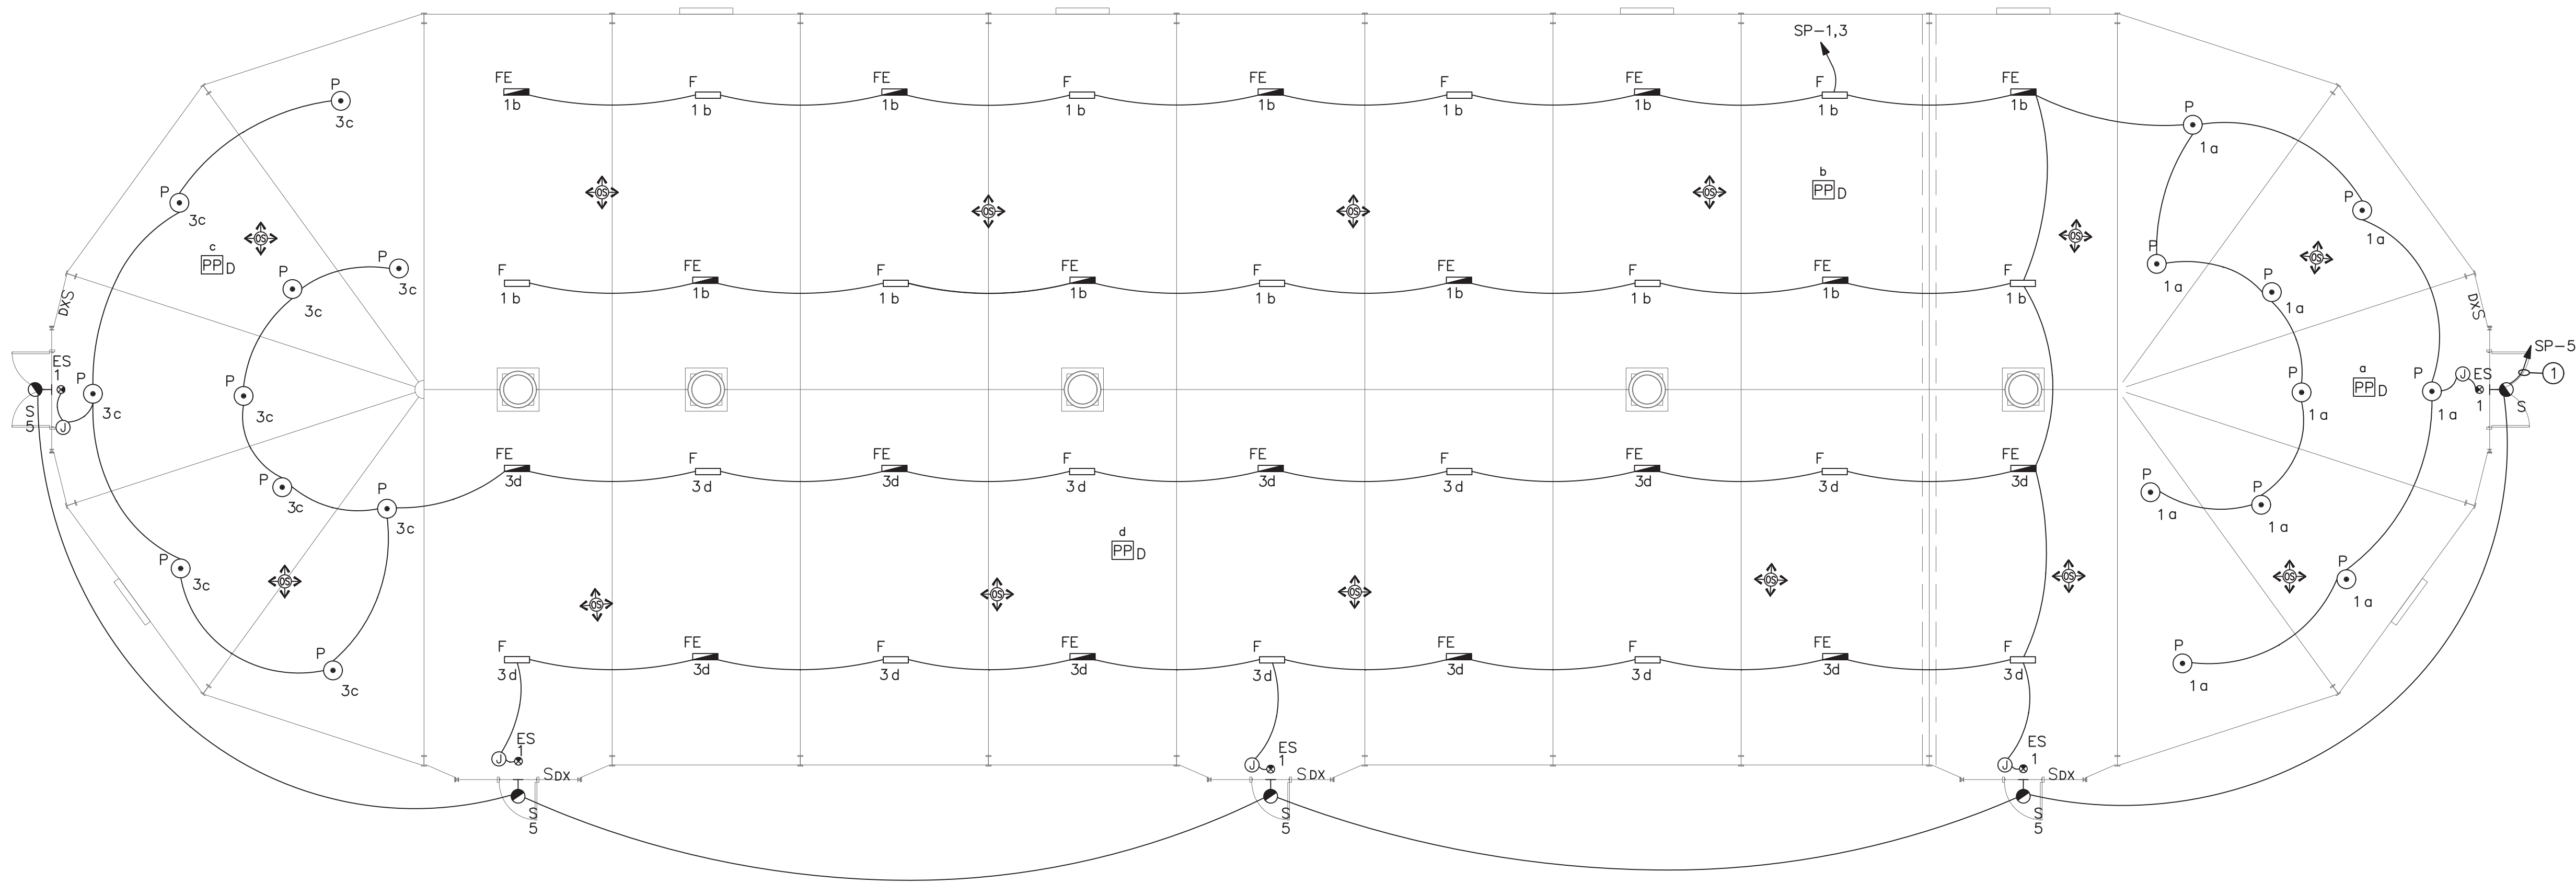

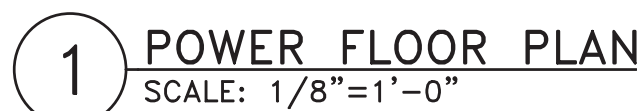POWER GENERAL NOTES

- A. ALL EXTERIOR DISCONNECTS SHALL BE W.P. TYPE.
- B. ALL RECEPTACLES WITHIN 6'-0" OF A SINK TO BE GFCI RATED.
- C. REFER TO MECHANICAL AND PLUMBING PLANS FOR EXACT SIZE, LOCATION, AND ELECTRICAL REQUIREMENTS FOR ALL MECHANICAL AND PLUMBING EQUIPMENT.
- D. ELECTRICAL CONTRACTOR SHALL FIELD VERIFY ALL CONNECTION REQUIREMENTS (HP, AMPS, VOLTAGE, PHASE, MOUNTING HEIGHT, AND DISCONNECT MEANS) FOR ALL EQUIPMENT SUPPLIED BY OTHERS BEFORE ROUGH-IN. DISCONNECT SWITCHES SHALL BE LOCATED WITH NEC CODE CLEARANCE OR PROVIDE LOCKOUT TYPE C/B.
- E. ELECTRICAL CONTRACTOR RESPONSIBLE FOR COORDINATING EXACT LOCATION, QUANTITIES, AND INSTALLATION REQUIREMENTS OF ELECTRICAL EQUIPMENT IN MILL WORK.
- F. ALL EXTERIOR RECEPTACLES SHALL BE W.P./GFCI TYPE.
- G. ALL ELECTRICAL PANEL BOARDS SHALL MAINTAIN 3'-0" INFRONT WORKING CLEARANCE REFER TO ONE-LINE FOR DETAILS.
- H. ELECTRICAL CONTRACTOR SHALL PROVIDE #6 COPPER GROUND TO ANY NEW METAL GAS PIPE SYSTEMS PER NEC 250.
- I. CONDUIT AND WIRING SHOWN FOR REFERENCE ONLY. IT IS THE RESPONSIBILITY OF THE ELECTRICAL CONTRACTOR TO PROVIDE THE NUMBER OF CONDUCTORS REQUIRED FOR HOT-LEGS, NEUTRAL AND GROUNDING AT EACH DEVICE FOR PROPER BRANCH CIRCUITING SHOWN FOR EACH AREA OR ROOM.

MECHANICAL GENERAL NOTES

- A. VERIFY ALL MECHANICAL UNIT LOCATIONS WITH MECHANICAL PLANS.
- B. THE ELECTRICAL CONTRACTOR SHALL NOT MOUNT DISCONNECT EQUIPMENT DIRECTLY TO MECHANICAL UNITS FOR DISCONNECTS 200A AND LARGER. THE ELECTRICAL CONTRACTOR SHALL PROVIDE A SELF-SUPPORTING SYSTEM FOR DISCONNECT EQUIPMENT.
- C. PROVIDE WEATHERPROOF, HEAVY DUTY, NEMA 3R FUSIBLE DISCONNECT SWITCHES FOR ALL MECHANICAL UNITS LOCATED OUTSIDE.
- D. ALL EXTERIOR RECEPTACLES SHALL BE WEATHER RESISTANT GFCI (PASS & SEYMOUR 2095DSWRBK OR EQUAL), INSTALLED IN A WEATHERPROOF ENCLOSURE WITH A WHILE IN USE COVERPLATE (PASS & SEYMOUR #WUC10CLO OR EQUAL).
- E. EXHAUST FANS MOUNTED OUTSIDE SHALL HAVE A WEATHERPROOF DISCONNECT MOUNTED EXTERIOR TO THE UNIT. INTERNAL DISCONNECT SWITCHES SHALL NOT BE ALLOWED.

2 KEYED NOTES

1. PROVIDE MAINTENANCE RECEPTACLE WITHIN 25' OF ALL MECHANICAL EQUIPMENT PER NEC 210.63.
2. PROVIDE 120V CONNECTION TO DUCT SMOKE DETECTORS INTERLOCK FOR SIMULTANEOUS UNIT SHUT-DOWN WITHIN 30 SECONDS OR LESS. VERIFY FINAL CONNECTION LOCATION AND REQUIREMENTS WITH MECHANICAL CONTRACTOR. TYPICAL.
3. PROVIDE PLUG LOAD CONTROL POWER PACK. COORDINATE EXACT LOCATION WITH OWNER/ARCHITECT PRIOR TO INSTALLATION. PLEASE REFER TO SHEET E1.0 FOR CORRESPONDING CEILING SENSOR.
4. PROVIDE PERMANENT MARKING TO IDENTIFY CONTROLLED RECEPTACLE.
5. PROVIDE RECEPTACLE/DATA & TELEPHONE FOR CHARGING STATIONS. COORDINATE OUTLET LOCATIONS & CONDUIT ROUTING WITH MILLWORK PRIOR TO INSTALLATION.



TOLL FREE: 1-800-528-9899
or (403) 601-2292 www.sprung.com



DESIGN LOADS

STRUCTURE LOCATION: HUNTINGTON BEACH, CA
BUILDING CODE: IBC 2018/CBC 2019
WIND SPEED: 106 mph 3 SEC GUST
RISK CATEGORY: II EXPOSURE C
GROUND SNOW LOAD: NA
(SEE SNOW SHED REPORT)



940 E Elm Avenue
Salt Lake City, Utah 84106
Phone: (801) 486-6848



SIGNATURE SERIES

[illegible]


REV	MM/DD/YY	BY	DESCRIPTION
-----	----------	----	-------------

This drawing is protected by copyright in the United States of America, Canada and all other countries of the world. It, and all of the designs, technical data and engineering services represented by it and originated or rendered by ©SPRUNG INSTANT STRUCTURES INC. are the exclusive property of ©SPRUNG INSTANT STRUCTURES INC. and must neither be used in manufacturing nor disclosed nor reproduced in whole or in part except with the prior written consent of ©SPRUNG INSTANT STRUCTURES INC. Any copying of this drawing in whole or in part and any use of it to construct the subject matter illustrated in it without prior written permission of ©SPRUNG INSTANT STRUCTURES INC. is prohibited.

17631 CAMERON LANE
HUNTINGTON BEACH, CA 92647

POWER
PLAN

DRAWN BY:	DATE: 08/19/2020
SCALE: AS NOTED	DRAWING # E2.0
SPRUNG WO: 24130	

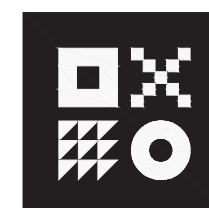

ARDEBILI
Engineering

Project Number: 20383 | Project Manager: FH
8100 E Indian School Rd. Suite 205, Scottsdale, AZ 85251
P: 480.626.7072 | ardebilieng.com



FAULT CURRENT SCHEDULE																	
DEVICE		FAULT	AIC RATING	L-N VOLTS	UTILITY	FED FROM		FEEDER						TOTAL MOTOR	DIRECTLY CONNECTED MOTOR LOAD		
					FAULT	DEVICE	FAULT	SIZE	X / 1000'	R / 1000'	LENGTH	X	R		FAULT	KVA	FAULT
	SES	43,468	65,000	120V	42,000			(2)#350kcmil	0.02	0.019		0	0	1,468			
F1	R1	6,006	10,000	120V	5,991	SES	42,000	#1	0.046	0.15	118'	0.0054	0.0177	15			
F2	R2	5,303	10,000	120V	5,292	SES	42,000	#1	0.046	0.15	135'	0.0062	0.0203	11			
F3	SP	10,017	22,000	120V	9,367	SES	42,000	#3/0	0.042	0.077	123'	0.0052	0.0095	650	55.7	619	
F4	T1	16,158	22,000	120V	15,801	SES	42,000	#3/0	0.042	0.077	62'	0.0026	0.0048	357	11.4	220	
F5	T2	10,170	22,000	120V	9,901	SES	42,000	#3/0	0.042	0.077	115'	0.0048	0.0089	269	11.4	220	
F6	T3	8,505	22,000	120V	8,252	SES	42,000	#3/0	0.042	0.077	143'	0.006	0.011	253	11.4	220	
F7	T4	21,875	22,000	120V	21,383	SES	42,000	#3/0	0.042	0.077	38'	0.0016	0.0029	492	11.4	220	

ONE LINE GENERAL NOTES

- A. SWITCHBOARD COMPONENTS, INCLUDING OVERCURRENT PROTECTIVE DEVICES SHALL BE FULLY RATED FOR THE AVAILABLE FAULT CURRENT SHOWN.
- B. PER NEC ARTICLE 110.22, PROVIDE IDENTIFICATION AT ENCLOSURE OF PANEL BOARDS WHERE BREAKERS ARE APPLIED IN SERIES COMBINATION, STATING: "CAUTION - SERIES COMBINATION SYSTEM RATED _____AMPS AVAILABLE. IDENTIFIED REPLACEMENT COMPONENTS REQUIRED." CONTRACTOR TO FILL IN BLANK WITH AVAILABLE FAULT CURRENT AS SHOWN ON ONE-LINE DIAGRAM.
- C. PER NEC ARTICLE 240.86(A), PROVIDE IDENTIFICATION AT EACH DISCONNECTING MEANS FEEDING DOWNSTREAM DEVICES APPLIED IN SERIES COMBINATION. PROVIDE NOTE INDICATING: "CAUTION - SERIES RATED DEVICES ARE FED FROM THIS REMOTE MAIN. _____AMPS AVAILABLE. IDENTIFIED REPLACEMENT COMPONENT REQUIRED." CONTRACTOR TO FILL IN BLANK WITH AVAILABLE FAULT CURRENT AS SHOWN ON ONE-LINE DIAGRAM.
- D. THE SERIES RATED SYSTEM WILL BE 2-TIER WITH DEVICES RATED @ 65K/14K FOR 480V SYSTEMS AND 65K/10K FOR 208V SYSTEMS. MOTOR SHORT CIRCUIT CONTRIBUTION IS LESS THAN 1% OF SYSTEM SHORT CIRCUIT AMPS.
- E. PROVIDE ARC FLASH AND SHOCK HAZARD WARNING IDENTIFICATION PER NEC ARTICLE 110.16
- F. "NO DESIGN CHANGES MAY BE MADE TO THE SYSTEM WITHOUT THE PRIOR APPROVAL OF THE DESIGN ENGINEER AND THE ELECTRICAL INSPECTOR."
- G. THE FEEDER LENGTHS SHOWN IN THE INPUT DATA IS FOR CALCULATIONS ONLY. IT IS NOT THE INTENT TO USE THESE ENTERED LENGTHS FOR USAGE OF ACTUAL FIELD FEEDER LENGTH MEASUREMENTS.

PANEL SCHEDULES GENERAL NOTES

- A. A.I.C. RATING SHOWN ON PANEL SCHEDULES ARE THE MINIMUM RATING FOR NEW AND REPLACEMENT OVERCURRENT PROTECTIVE DEVICES.
- B. ALL PANEL BOARDS SHALL HAVE A TYPE WRITTEN DIRECTORY IDENTIFYING EACH NUMBERED CIRCUIT PLACED IN A DIRECTORY HOLDER INSIDE THE DOOR.
- C. THE CONTRACTOR SHALL PERMANENTLY MARK WITH PERMANENT MARKER THE CIRCUIT IDENTIFICATIONS ON THE COVERPLATES OF RECEPTACLES, EQUIPMENT, AND LIGHTING JUNCTION BOXES. (STICK ON LABELS NOT ACCEPTABLE)
- D. PER NEC 210.4(B) ALL MULTIWIRE BRANCH CIRCUITS ARE TO BE PROVIDED WITH A DEVICE THAT WILL DISCONNECT POWER TO ALL UNGROUNDED CONDUCTORS SIMULTANEOUSLY AT THE POINT OF ORIGIN.

2 KEYED NOTES

1. PANEL SHALL BE LISTED AS SUSE RATED, SUITABLE FOR USE AS SERVICE EQUIPMENT, WITH MAIN CIRCUIT BREAKER -LOCATION TO COMPLY WITH NEC 230.70 (A)(1). DO NOT BOND THE NEUTRAL AND GROUND BUS AS THIS HAS BEEN DONE UPSTREAM AT ITS SOURCE.

S.U.S.E

SUITABLE FOR USE AS SERVICE EQUIPMENT
(FOR SERVICES ON THE LOAD SIDE OF THE
MAIN SERVICE ENTRANCE DISCONNECT PER
NEC 230.66)

SES

ROOM SITE				VOLTS 208Y/120V 3P 4W				AIC 65,000			
MOUNTING FLOOR				BUS AMPS 600				MAIN BKR 600			
FED FROM UTILITY				NEUTRAL 100%				LUGS STANDARD			
NOTE NEMA-3R											

CKT #	CIRCUIT DESCRIPTION	KVA LOAD			FRAME TRIP / POLES	COND.	FEEDER RACEWAY AND CONDUCTORS					
		A	B	C								
1	FUSED DISCONNECT D1	1.56	1.56		30/2	3/4"C,2#8,#8G						
2	FUSED DISCONNECT D2	1.56	1.56		30/2	3/4"C,2#8,#8G						
3	PANEL R1	4.16	4.16		100/2	1-1/4"C,3#1,#8G						
4	PANEL R2	4.16	4.16		100/2	1-1/4"C,3#1,#8G						
5	FUSED DISCONNECT RMO	2.08	2.08		30/2	3/4"C,2#8,#8G						
6	PANEL SP	21.9	20	19.8	200/3	2"C,4#3/0,#8G						
7	PANEL T1	10.4	10.2		150/2	2"C,3#3/0,#4G						
8	PANEL T2	10.4	10.2		150/2	2"C,3#3/0,#4G						
9	PANEL T3	10.4	10.2		150/2	2"C,3#3/0,#4G						
10	PANEL T4	10.4	10.2		150/2	2"C,3#3/0,#4G						
11	SPACE	0	0	0	- /3							
TOTAL CONNECTED KVA BY PHASE		76.9	74.2	19.8								

NEW S.E.S.



innovation | versatility | reliability

TOLL FREE: 1-800-528-9899
or (403) 601-2292 www.sprung.com




DESIGN LOADS

STRUCTURE LOCATION: HUNTINGTON BEACH, CA
BUILDING CODE: IBC 2018/CBC 2019
WIND SPEED: 106 mph 3 SEC GUST
RISK CATEGORY: II EXPOSURE C
GROUND SNOW LOAD: NA
(SEE SNOW SHED REPORT)



940 E Elm Avenue
Salt Lake City, Utah 84106
Phone: (801) 486-6848

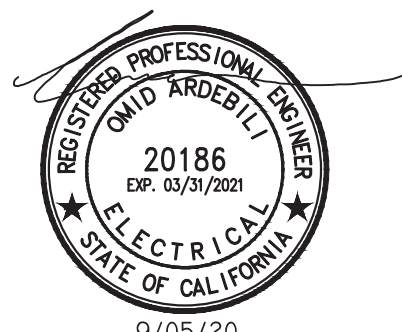

9/05/20

SIGNATURE SERIES

[illegible]


REV	MM/DD/YY	BY	DESCRIPTION
-----	----------	----	-------------

This drawing is protected by copyright in the United States of America, Canada and all other countries of the world. It, and all of the designs, technical data and engineering services represented by it and originated or rendered by ©SPRUNG INSTANT STRUCTURES INC. are the exclusive property of ©SPRUNG INSTANT STRUCTURES INC. and must neither be used in manufacturing nor disclosed nor reproduced in whole or in part except with the prior written consent of ©SPRUNG INSTANT STRUCTURES INC. Any copying of this drawing in whole or in part and any use of it to construct the subject matter illustrated in it without prior written permission of ©SPRUNG INSTANT STRUCTURES INC. is prohibited.

17631 CAMERON LANE
HUNTINGTON BEACH, CA 92647

ONE LINE DIAGRAM

DRAWN BY:	DATE: 08/19/2020
SCALE: AS NOTED	DRAWING #
SPRUNG WO: 24130	E3.0

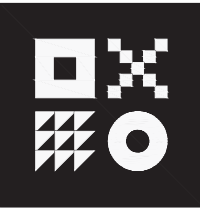

ARDEBIL
Engineering

Project Number: 20383 | Project Manager: FH
8100 E Indian School Rd. Suite 205, Scottsdale, AZ 85258
P: 480.626.7072 | ardebilieng.com

SP

NEW PANEL											
ROOM EXTERIOR				VOLTS 208Y/120V 3P 4W				AIC 22,000			
MOUNTING FLOOR				BUS AMPS 200				MAIN BKR 200			
FED FROM SES				NEUTRAL 100%				LUGS STANDARD			
NOTE NEMA 3R											
CKT #	CKT BKR	CIRCUIT DESCRIPTION	KVA LOAD			CKT #	CKT BKR	CIRCUIT DESCRIPTION	KVA LOAD		
			A	B	C				A	B	C
1	20/1	INTERIOR-1 LIGHTING	0.773			2	30/1	(E)EF-3	2.88		
3	20/1	INTERIOR-2 LIGHTING		0.776		4	30/1	(E)EF-3		2.88	
5	20/1	EXTERIOR-1 LIGHTING			0.13	6	30/1	(E)EF-3			2.88
7	20/2	EXTERIOR-2 LIGHTING	0.191			8	20/2	EF-1	1.25		
9				0.191		10				1.25	
11	20/1	1- RECEPTACLE			0.72	12	20/2	EF-2			1.25
13	20/1	2- RECEPTACLE	0.72			14			1.25		
15	20/1	3- RECEPTACLE		0.36		16	90/3	RTU-1		7.01	
17	20/1	1-CONTROLLED RECEPTACLE			0.18	18					7.01
19	20/1	4- RECEPTACLE	0.36			20			7.01		
21	20/1	2-CONTROLLED RECEPTACLE		0.18		22	20/1	MAINTENANCE RECEPTACLE		0.36	
23	20/2	EXTERIOR-3 LIGHTING			0.504	24	20/1	DUCT DETECTOR			0.1
25			0.504			26	90/3	RTU-2	7.01		
27	-/1	SPACE		0		28				7.01	
29	-/1	SPACE			0	30					7.01
31	-/1	SPACE	0			32	-/1	SPACE	0		
33	-/1	SPACE		0		34	-/1	SPACE		0	
35	-/1	SPACE			0	36	-/1	SPACE			0
37	-/1	SPACE	0			38	-/1	SPACE	0		
39	-/1	SPACE		0		40	-/1	SPACE		0	
41	-/1	SPACE			0	42	-/1	SPACE			0
TOTAL CONNECTED KVA BY PHASE									21.9	20	19.8
TOTAL CONNECTED AMPS BY PHASE									183	167	165
			CONN KVA	CALC KVA					CONN KVA	CALC KVA	
LIGHTING			3.07	3.84	(125%)	MOTORS			55.7	55.7	(100%)
LARGEST MOTOR			21	5.26	(25%)	RECEPTACLES			2.88	2.88	(50%>10)
						NONCONTINUOUS			0.1	0.1	(100%)
						TOTAL LOAD				67.8	
						BALANCED 3-PHASE LOAD				188 A	

NEW PANEL

T1

EXISTING PANEL									
ROOM			VOLTS 208/120V 2P 3W				AIC 22,000		
MOUNTING FLUSH			BUS AMPS 150				MAIN BKR 150		
FED FROM SES			NEUTRAL 100%				LUGS STANDARD		
NOTE									
CKT #	CKT BKR	CIRCUIT DESCRIPTION	KVA LOAD		CKT #	CKT BKR	CIRCUIT DESCRIPTION	KVA LOAD	
			A	B				A	B
1	60/2	EXISTING A/C	5.72		2	20/1	EXISTING RECEPTACLE	1.08	
3				5.72	4	20/1	EXISTING RECEPTACLE/CLOCK		1.08
5	60/2	SPARE	0		6	20/1	EXISTING COMP. RECEPTACLE	1.08	
7				0	8	20/1	EXISTING COMP. RECEPTACLE		1.08
9	20/1	EXISTING LIGHTING	1.2		10	20/1	EXISTING COMP. RECEPTACLE	1.08	
11	20/1	EXISTING LIGHTING		1.2	12	20/1	EXISTING COMP. RECEPTACLE		1.08
13	15/1	EXISTING ALARM	0.2		14	-/1	SPACE	0	
15	-/1	SPACE		0	16	-/1	SPACE		0
TOTAL CONNECTED KVA BY PHASE								10.4	10.2
TOTAL CONNECTED AMPS BY PHASE								90.6	89
			CONN KVA	CALC KVA				CONN KVA	CALC KVA
LIGHTING			2.4	3	(125%)			MOTORS	11.4
LARGEST MOTOR			11.4	2.86	(25%)			RECEPTACLES	6.48
								NONCONTINUOUS	0.2
								TOTAL LOAD	24
								BALANCED LOAD	115 A

TYPICAL FOR PANELS T1, T2, T3, T4



TOLL FREE: 1-800-528-9899
or (403) 601-2292 www.sprung.com



DESIGN LOADS

STRUCTURE LOCATION:HUNTINGTON BEACH, CA
BUILDING CODE: IBC 2018/CBC 2019
WIND SPEED: 106 mph 3 SEC GUST
RISK CATEGORY: II EXPOSURE C
GROUND SNOW LOAD: NA
(SEE SNOW SHED REPORT)



940 E Elm Avenue
Salt Lake City, Utah 84106
Phone: (801) 486-6848



9/05/20

SIGNATURE SERIES

REV	MM/DD/YY	BY	DESCRIPTION
This drawing is protected by copyright in the United States of America, Canada and all other countries of the world. It, and all of the designs, technical data and engineering services represented by it and originated or rendered by SPRUNG INSTANT STRUCTURES INC. are the exclusive property of SPRUNG INSTANT STRUCTURES INC. and must neither be used in manufacturing nor disclosed nor reproduced in whole or in part except with the prior written consent of SPRUNG INSTANT STRUCTURES INC. Any copying of this drawing in whole or in part and any use of it to construct the subject matter illustrated in it without prior written permission of SPRUNG INSTANT STRUCTURES INC. is prohibited.			

17631 CAMERON LANE
HUNTINGTON BEACH, CA 92647


PANEL
SCHEDULES

DRAWN BY:	DATE:
SCALE:	DRAWING #
SPRUNG WO:	

08/19/2020

AS NOTED

E3.1

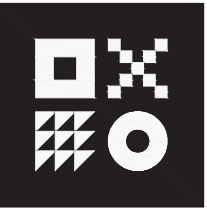

ARDEBILI
Engineering

Project Number: 20393 | Project Manager: FH
8190 E Indian School Rd. Suite 205, Scottsdale, AZ 85251
P: 480.626.7072 | ardebilieng.com