


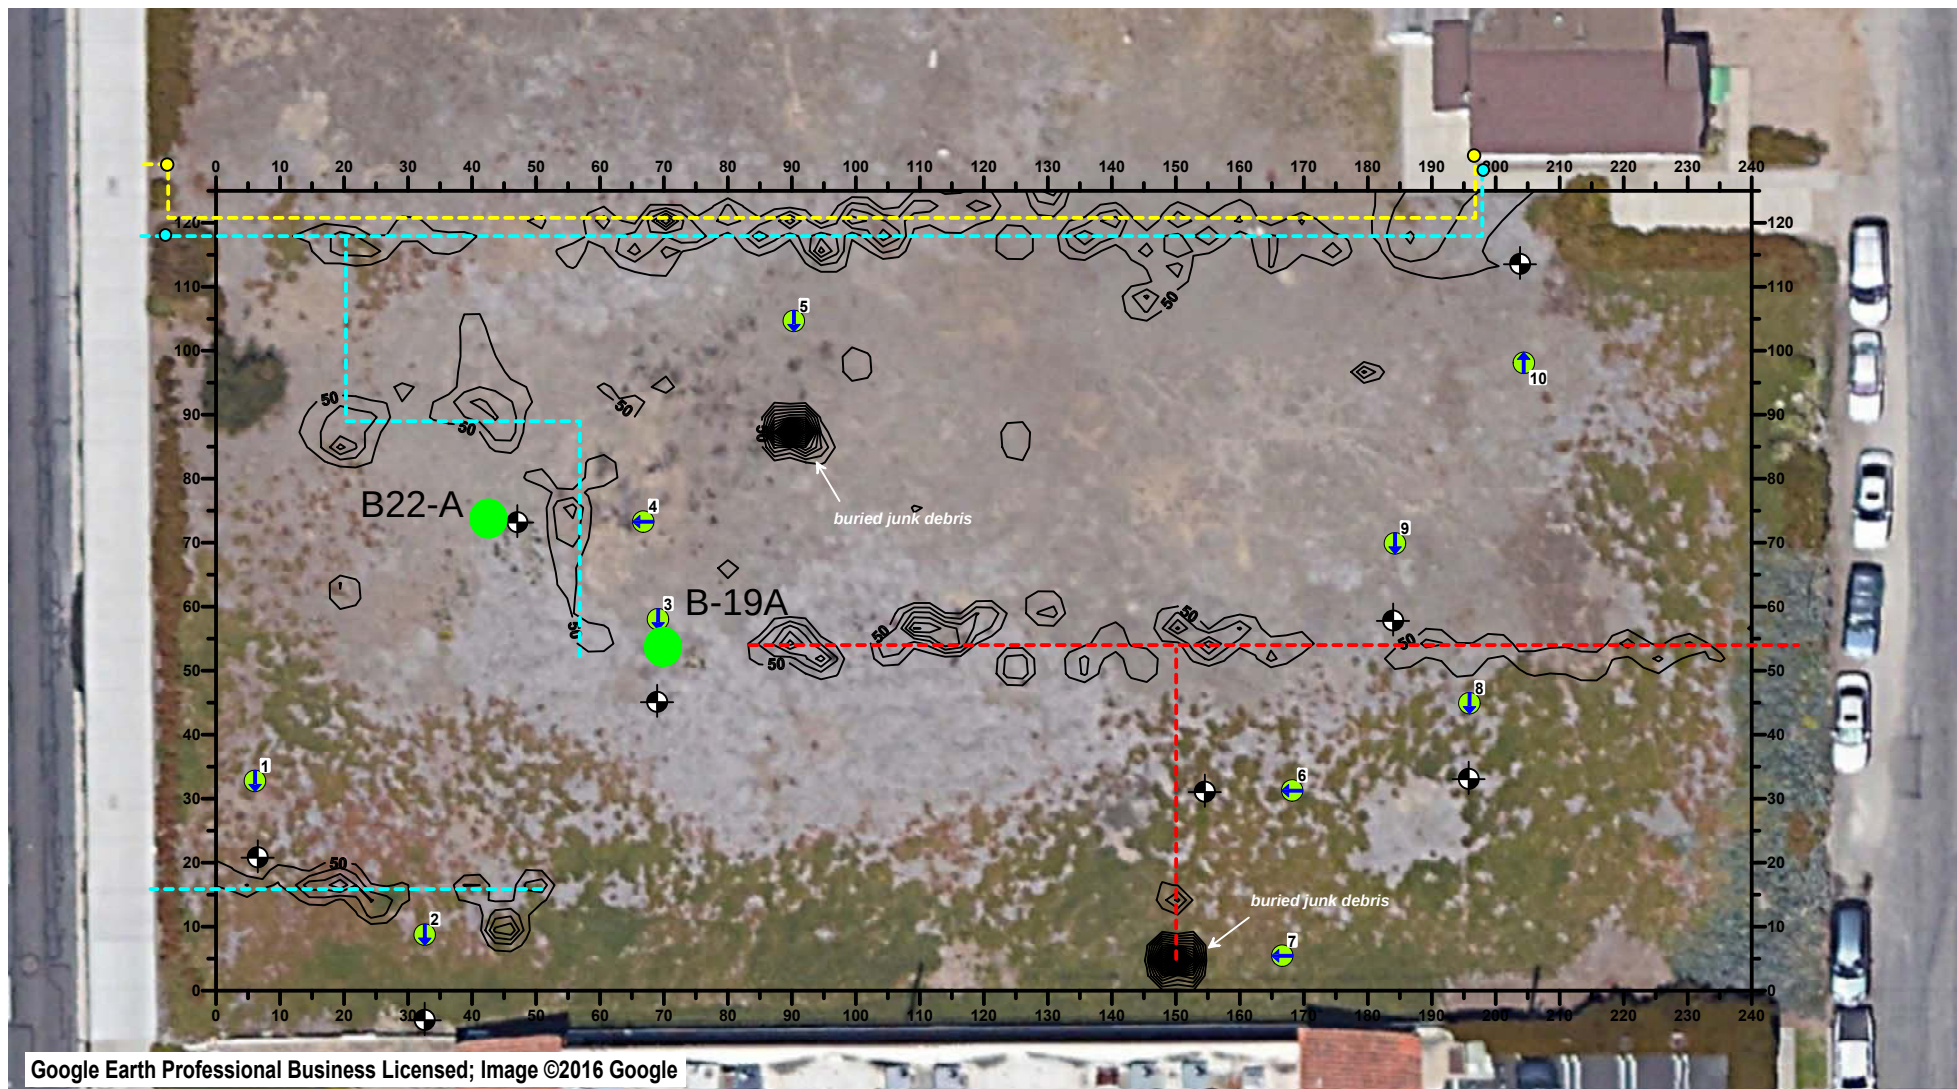

	SITE: 17631 Cameron Ln Huntington Beach, California	TITLE: Site Interpretation Map	DATE: April 13th, 2020
		PREPARED FOR: EEC	SSS PROJECT NO: 20-164
LEGEND:			
	gas line		gas riser
	water line		water riser
	electric line		vantage angle of photo
			proposed borehole
			contour lines
EM-61 GRID Contour Interval = 50 mVolts			
			SCALE  0 ~30'
FIGURE 3			